ANWANDER

BRANDSCHUTZ-NACHWEIS

⊕ ABWEICHUNGSANTRAG

ALTE MOLKEREI - EINBAU VON GESCHÄFTS- UND BÜRORÄUMEN

Flst. Nr.98 , Gemarkung Erkheim

Marktstraße 5

87746 Erkheim

BAUHERR

Norbert Mayer u. Prof. Dr. Achim Dehnert

Falchenweg 32

87746 Erkheim

PLANVERFASSER

Achitekturbüro Füss

Sonthofener Straße 26

87545 Burgberg

06.02.2019 2717-01/01

INHALTSVERZEICHNIS

A BRANDSCHUTZNACHWEIS 5

1 ALLGEMEINES 5
1.1 AUFTRAG, UNTERLAGEN UND BETRACHTUNGSUMFANG 5
1.1 NUTZUNG DES GEBÄUDES 7
1.2 BAUBESCHREIBUNG 7
1.3 GEFÄHRDUNGSBEWERTUNG 8
1.4 SCHUTZZIELE 8
1.5 BESCHREIBUNG UND GESTALTUNG DES NACHWEISES 8
2 BAUORDNUNGSRECHTLICHE BEURTEILUNGSGRUNDLAGE 11
2.1 GEBÄUDEEINSTUFUNG NACH BAYERISCHER BAUORDNUNG 11
2.2 ANWENDBARE SONDERBAUVORSCHRIFTEN 11
2.3 PRÜFUNG DES BRANDSCHUTZNACHWEISES 11
2.4 BAUART UND -PRODUKTE 11
2.5 WEITERE VORSCHRIFTEN UND RICHTLINIEN 11
3 ABWEHRENDER BRANDSCHUTZ 13
3.1 FLÄCHEN FÜR DIE FEUERWEHR 13
3.2 ABSTANDSFLÄCHEN UND BRANDSCHUTZABSTÄNDE 14
3.3 LÖSCHWASSERVERSORGUNG 14
3.4 RAUCHABLEITUNG 14
3.4.1. KELLER 14
3.4.2. NOTWENDIGER TREPPENRAUM 15
3.4.3. AUFZUG 15
4 BAULICHER BRANDSCHUTZ 16
4.1 BRANDABSCHNITTE, BRANDWÄNDE 16
4.2 ANFORDERUNGEN AN WESENTLICHE BAUTEILE 17
4.2.1. TRAGENDE UND AUSSTEIFENDE WÄNDE UND STÜTZEN 17
4.2.2. DECKEN 18
4.2.3. AUßENWÄNDE 19
4.2.4. TRENNWÄNDE 20
4.2.5. DÄCHER 21
4.3 RETTUNGSWEGE 22
4.3.1. ANZAHL, VERLAUF UND AUSGÄNGE 22
4.3.2. RETTUNGSWEGLÄNGEN 23
4.3.3. RETTUNGSWEGBREITEN 23
4.3.4. NOTWENDIGE TREPPEN 24
4.3.5. NOTWENDIGE TREPPENRÄUME 24
4.3.6. NOTWENDIGE FLURE 25

4.3.7. RETTUNGSWEGE ÜBER FENSTER ... 27
4.3.8. TÜREN IN RETTUNGSWEGEN ... 28
5 ANLAGENTECHNISCHER BRANDSCHUTZ ... 29
5.1 ALLGEMEINE TECHNISCHE GEBÄUDEAUSRÜSTUNG ... 29
5.1.1. AUFZUG ... 29
5.1.2. LEITUNGSANLAGEN SOWIE INSTALLATIONSSCHÄCHTE UND -KANÄLE ... 29
5.1.3. LÜFTUNGSANLAGEN ... 30
5.1.4. FEUERUNGSANLAGEN, SONSTIGE WÄRMEERZEUGER UND BRENNSTOFFVERSORGUNG ... 31
5.1.5. RÄUME ZUR AUFBEWAHRUNG FESTER ABFALLSTOFFE ... 31
5.1.6. ELEKTRISCHE BETRIEBSRÄUME ... 31
5.2 SICHERHEITSTECHNISCHE GEBÄUDEAUSRÜSTUNG ... 31
5.2.1. BLITZSCHUTZANLAGEN ... 31
5.2.2. RAUCHWARNMELDER ... 31
5.2.3. RETTUNGSWEGKENNZEICHNUNG ... 32
5.2.4. SICHERHEITSBELEUCHTUNG ... 32
5.2.5. BRANDMELDE- UND ALARMIERUNGSANLAGEN ... 32
5.2.6. FEUERLÖSCHEINRICHTUNGEN UND -ANLAGEN ... 32
5.2.7. SICHERHEITSSTROMVERSORGUNG ... 32
5.2.8. FESTSTELLANLAGEN ... 32
5.2.9. PRÜFUNG SICHERHEITSTECHNISCHER EINRICHTUNGEN ... 32
6 ORGANISATORISCHER BRANDSCHUTZ ... 34
B ABWEICHUNGSANTRAG ... 35
7 GENEHMIGUNGSPFLICHTIGE ABWEICHUNGEN ... 35
7.1 ABWEICHUNG VON KAPITEL 4.3.5 - NOTWENDIGE TREPPENRÄUME ... 35

ABBILDUNGSVERZEICHNIS

Abbildung 1: Auszug Lageplan - Betrachtungsbereich ... 5
Abbildung 2: Auszug Grundriss ERdgeschoss ... 6
Abbildung 3: Baueingabe Kellergeschoss ... 6
Abbildung 4: Lageplan - Feuerwehranfahrt ... 13
Abbildung 5: Grundriss Kellergeschoss ... 15
Abbildung 6: Auszug Lageplan mit Grundstücksgrenze ... 16
Abbildung 7: BSK 2014 (Thmoas Kreiter) – Obergeschoss ... 17
Abbildung 8: Ansicht Ost - Dächer von Anbauten ... 21
Abbildung 9: Rettungsweg KG Büro 1 ... 22
Abbildung 10: RW-Führung Kellergeschoss ... 22
Abbildung 11: RW-Führung Erdgeschoss ... 23

Abbildung 12: Auszug BSK 2014 (Thmomas Kreiter) - Treppenraum Erdgeschoss 25

Abbildung 13: Auszug BSK 30.01.2019 - Erdgeschoss 26

A BRANDSCHUTZNACHWEIS

1 ALLGEMEINES

1.1 AUFTRAG, UNTERLAGEN UND BETRACHTUNGSUMFANG

Das Ingenieurbüro Anwander GmbH & Co. KG wurde beauftragt, den Brandschutznachweis im Rahmen des Art. 64 BayBO bzw. Art. 62 BayBO und § 11 BauVorlV zu erstellen.

Folgende Unterlagen wurden hierzu vom Planverfasser Füss Architekten als Grundlage zur Verfügung gestellt:

Plan	Maßstab	Stand
Grundrisse EG, KG	1:100	17.07.2018
Grundriss KG Bestand	/	/
Schnitte A,	1:100	17.07.2018
Ansichten Nord, Ost, Süd,	1:100	17.07.2018
Lageplan	1:1000	17.07.2018

Die Grundrisse, Ansichten und Schnitte wurden in digitaler Form übersandt.

Im vorliegenden Brandschutznachweis wird die Nutzungsänderung im Erdgeschoss des Bestandsgebäudes der alten Molkerei betrachtet. Im Zuge der Nutzungsänderung sollen die zuvor genutzten Lagerräume zu zwei Büronutzungseinheiten (BGF ca. 120 m² und 183 m²) umgenutzt werden.

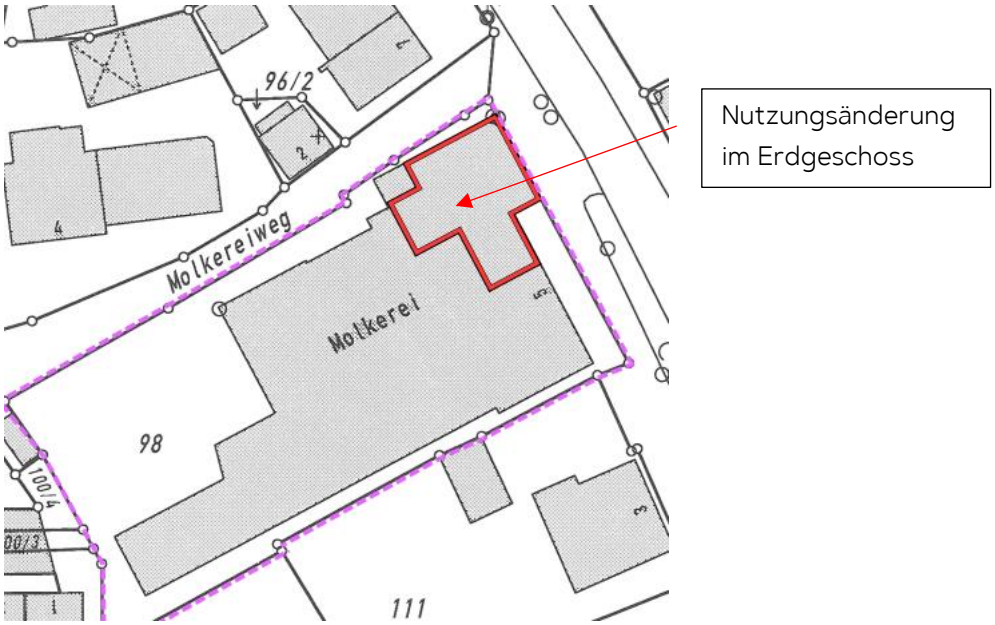

Abbildung 1: Auszug Lageplan - Betrachtungsbereich

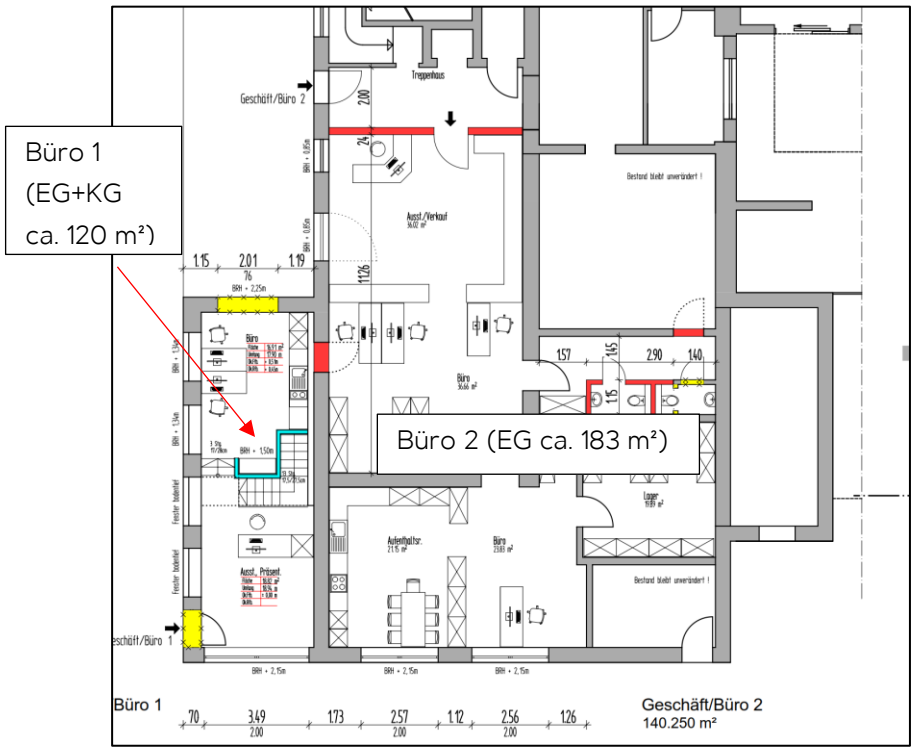

Abbildung 2: Auszug Grundriss ERdgeschoss

Die kleine Büroeinheit „Büro 1" bekommt einen direkten Zugang von außen sowie eine neue Treppe in das Kellergeschoss mit direkter Erschließung eines Lagerraums. Im benachbarten Kellerbereich sollen weiterhin drei WC-Räume eingebaut werden. Der Einbau der WC-Räume im Bestandskeller ist brandschutztechnisch unrelevant und wird daher nicht weiter betrachtet. Aufenthaltsräume befinden sich in dem hier betrachteten Kellerbereich nicht und sind auch nicht zulässig.

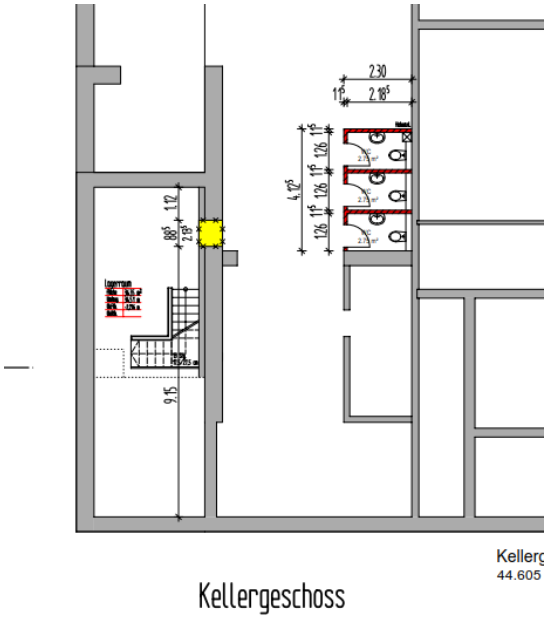

Abbildung 3: Baueingabe Kellergeschoss

Weiterhin sind neue Fenster für die beiden Nutzungseinheiten geplant sowie die Ausbildung einer Trennwand zwischen den beiden Nutzungseinheiten.

Weitere bauliche Maßnahmen/Veränderungen im Bestand sind nicht geplant. Im restlichen Bestandsgebäude befindet sich eine ambulant betreute Wohngemeinschaft, die 2014 genehmigt wurde. Der Brandschutznachweis inkl. Konzeptpläne von 2014, erstellt durch Herrn Kreiter Thomas liegt dem Nachweisersteller vor und wird entsprechend berücksichtigt. Der entsprechende Bescheid „Brandschutz I" liegt nicht vor.

Alle weiteren Gebäudeteile liegen außerhalb des Beurteilungsumfangs und werden im Rahmen dieses Brandschutznachweises nicht bewertet. Bei diesen handelt es sich nach Vorgaben des Bauherrn bzw. Architekten um genehmigten Bestand. Durch die Umbaumaßnahmen ergeben sich keine erhöhten Anforderungen an die bestehenden Nutzungen, wodurch keine erneute brandschutztechnische Beurteilung erforderlich ist (s. auch Schreiben der Obersten Baubehörde vom 25.07.2011, AZ: IIB7-4112.420-013/11).

1.1 NUTZUNG DES GEBÄUDES

Der hier betrachtete Gebäudebereich ist nach Angaben des Bauherrn bzw. Architekten öffentlich zugänglich. Die Belange der Barrierefreiheit sind deshalb nach Art. 48 BayBO zu berücksichtigen. Auf Grund der nicht hauptsächlichen und nicht vorhersehbaren Nutzung des Gebäudes durch Menschen mit Einschränkungen werden im vorliegenden Brandschutznachweis keine konkreten brandschutztechnischen Maßnahmen diesbezüglich beschrieben.

Nutzeranzahl

Die hier betrachteten Büronutzungen verfügen jeweils über 3 bis 5 Arbeitsplätzen.

Nutzerqualität

Die Nutzer sind in der Regel , selbstständig, ortskundig, normal beweglich und ständig aufmerksam (keine Schlafstätten).

1.2 BAUBESCHREIBUNG

Im Zuge der hier betrachteten Nutzungsänderung (EG, KG) finden keine Eingriffe in die Tragkonstruktion/ Umfassungsbauteile des Bestandes statt. Der Bestand (KG, EG, OG) wurde gem. BSN 2014 massiv in Stahlbeton/ Mauerwerk errichtet.

Allgemeine Objektdaten Nutzungsänderung:

max. Gebäudelänge: ca. 18 m

max. Gebäudebreite: ca. 18 m

Gebäudehöhe: erdgeschossig
(Fußbodenoberkante im höchsten Geschoss, in dem ein Aufenthaltsraum möglich ist, zur mittl. Geländeoberfläche)

Grundfläche größtes Geschoss: ca. 258 m²
(Grundfläche des Geschosses mit der größten Ausdehnung)

1.3 GEFÄHRDUNGSBEWERTUNG

Es ist keine erhöhte Brandentstehungs- oder Explosionsgefahr im hier betrachteten Bereich vorhanden.

Die bauliche Brandlast ist aufgrund der Bauweise als erhöht anzusehen. Im Gebäude ist außerdem von der Nutzung entsprechend normalen Verkehrsbrandlasten auszugehen.

Die Brandentstehungsrisiken durch Elektroanlagen, menschliches Versagen, technische Unzulänglichkeiten, Naturereignisse und Selbstentzündung sind durchwegs als normal anzusehen.

Besondere Gefahrstoffe sind im Gebäude nicht vorhanden.

1.4 SCHUTZZIELE

Die Schutzziele sind in Art. 12 BayBO definiert.

> *Art. 12 BayBO*
>
> *Bauliche Anlagen sind so anzuordnen, zu errichten, zu ändern und instand zu halten, dass der* ***Entstehung eines Brandes*** *und der* ***Ausbreitung von Feuer und Rauch*** *(Brandausbreitung) vorgebeugt wird und bei einem Brand die* ***Rettung von Menschen und Tieren*** *sowie* ***wirksame Löscharbeiten*** *möglich sind*

- Vorbeugung der Brandentstehung
- Personenrettung im Brandfall
- Vorbeugung der Brandausbreitung
- Ermöglichen eines risikoarmen und erfolgreichen Löschangriffs
- Sachschutz im Rahmen des Bauordnungsrechtes

Versicherungstechnische Belange des Brandschutzes **sowie Belange der Arbeitssicherheit** werden im Rahmen dieses Brandschutznachweises nicht bewertet.

1.5 BESCHREIBUNG UND GESTALTUNG DES NACHWEISES

Alle Inhalte dieses Dokuments, insbesondere Texte, Fotografien und Grafiken, sind urheberrechtlich geschützt. Das Urheberrecht liegt, soweit nicht ausdrücklich anders gekennzeichnet, beim Ingenieurbüro Anwander. Dieses Schriftstück ist ausschließlich mit den auf der letzten Seite genannten Anlagen zu verwenden. Es darf zudem nur ungekürzt vervielfältigt und nicht auf andere Bauobjekte übertragen werden. Eine auszugsweise oder gekürzte Verwendung bedarf der vorherigen schriftlichen Genehmigung des Verfassers.

Der Brandschutznachweis wird im Soll / Ist – Vergleich auf die Übereinstimmung des Bauvorhabens mit den gesetzlichen Vorgaben durchgeführt.

Eine schutzzielorientierte Betrachtung findet statt, wenn die gesetzlichen Vorgaben nicht eingehalten werden können und Abweichungen beantragt werden. Gesetzestext sowie Texte von Vorschriften und/oder Richtlinien, werden in vorliegendem Brandschutznachweis *grau und kursiv* gekennzeichnet und mit der Quellenangabe versehen.

Die ausführliche Beschreibung erfolgt im Textteil. Ergänzende Pläne mit brandschutzrelevanten Eintragungen und weitere Anlagen werden dem Brandschutznachweis gegebenenfalls ergänzend beigelegt.

Es werden die **Anforderungen des vorbeugenden (baulich, anlagentechnisch, organisatorisch) und abwehrenden Brandschutzes** behandelt. Die zur Wahrung dieser Belange dienenden, allgemein anerkannten Regeln der Technik sind zu beachten. Von diesen kann nur abgewichen werden, wenn eine andere Lösung in gleicher Weise die allgemeinen Anforderungen erfüllt. Sollten Explosionsgefahren vorhanden sein, sind diese gesondert zu untersuchen.

Darüberhinausgehende bauordnungsrechtliche Themen, wie z. B. Abstandsflächen, oder die Anforderungen an Arbeitssicherheit werden in diesem Brandschutznachweis nicht behandelt.

Weitergehende Schutzziele (z.B. Objektschutz) bzw. versicherungstechnische Belange sind ebenfalls nicht Gegenstand des Nachweises.

Tragende, unterstützende und aussteifende Bauteile sind in den gegebenenfalls den Anlagen beigefügten Brandschutzkonzeptplänen **nicht farblich dargestellt** und einer Feuerwiderstandsdauer zugeordnet. Die Anforderungen sind aus dem Textteil des Brandschutznachweises zu entnehmen. Die Festlegung, welche Elemente tragende und aussteifende Bauteile sind, ist durch den zuständigen Tragwerksplaner zu treffen.

Es sind **nur raumabschließende Wände** in den Brandschutzkonzeptplänen - sofern in der Anlage vorhanden - **farblich dargestellt!**

Für die Klassifizierung der Feuerwiderstandsdauer von Bauteilen und der Brennbarkeit von Baustoffen werden im Brandschutznachweis die Begrifflichkeiten der BayBO verwendet (Art. 24 BayBO = **bauaufsichtliche Anforderung**).

Erforderliche genehmigungspflichtige Abweichungen nach Art. 63 BayBO werden im Text beschrieben und in Teil B nochmals zusammengestellt und begründet.

Nachfolgend sind die Begrifflichkeiten, in Anlehnung an die Ausführungen der BayTB zur DIN 4102, dargestellt:

Baustoffklassen

Die in der Norm angegebenen Baustoffklassen entsprechen den folgenden bauaufsichtlichen Anforderungen:

Bauaufsichtliche Anforderung	Baustoffklasse nach DIN 4102
nichtbrennbare Baustoffe	A A1 A2
brennbare Baustoffe schwerentflammbare Baustoffe normalentflammbare Baustoffe	B B1 B2
leichtentflammbare Baustoffe*	B3

* Leichtentflammbare Baustoffe (B3) dürfen gemäß Art. 24 Abs. 1 Satz 2 BayBO nicht verwendet werden, außer wenn sie in Verbindung mit anderen Baustoffen nicht leichtentflammbar sind.

Feuerwiderstandsdauer

Die in der Norm angegebenen Bezeichnungen entsprechen folgenden Anforderungen in bauaufsichtlichen Verwendungsvorschriften:

Bauaufsichtliche Anforderung	Benennung nach DIN 4102	Kurzbezeichnung
feuerhemmend	Feuerwiderstandsklasse F 30	F 30 - B
feuerhemmend und aus nichtbrennbaren Baustoffen	Feuerwiderstandsklasse F 30 und aus nichtbrennbaren Baustoffen	F 30 - A
hochfeuerhemmend*	Feuerwiderstandsklasse F 60 und in wesentlichen Teilen aus nicht-brennbaren Baustoffen	F 60 - AB
	Feuerwiderstandsklasse F 60 und aus nichtbrennbaren Baustoffen	F 60 - A
feuerbeständig	Feuerwiderstandsklasse F 90 und in wesentlichen Teilen aus nicht-brennbaren Baustoffen	F 90 - AB
feuerbeständig und aus nichtbrennbaren Baustoffen	Feuerwiderstandsklasse F 90 und aus nichtbrennbaren Baustoffen	F 90 - A

* Die Feuerwiderstandsfähigkeit von nach bauaufsichtlichen Anforderungen hochfeuerhemmenden Bauteilen, deren tragende und aussteifende Teile aus brennbaren Baustoffen bestehen und die allseitig eine brandschutztechnisch wirksame Bekleidung aus nichtbrennbaren Baustoffen haben müssen, kann nicht nach DIN 4102-2 nachgewiesen werden und ist deshalb in der Tabelle nicht aufgeführt.

Zur Übersetzung der Feuerwiderstandsklassen gemäß DIN 4102 auf die europäischen Feuerwiderstandsklassen gemäß DIN EN 13501 wird auf Anhang 4 Abschnitt 4 BayTB verwiesen. Für das Brandverhalten von Baustoffen gemäß DIN EN 13501-1 ist der Anhang 4 Abschnitt 1 BayTB anzuwenden.

2 BAUORDNUNGSRECHTLICHE BEURTEILUNGSGRUNDLAGE

2.1 GEBÄUDEEINSTUFUNG NACH BAYERISCHER BAUORDNUNG

vom 14.08.2007 – gültig seit 01.01.2008 – Stand: letzte berücksichtigte Änderung vom 10.07.2018

Beim betrachteten Bauvorhaben handelt es sich nach Art. 2 Abs. 3 und Abs. 4 BayBO um ein Gebäude der

Gebäudeklasse 3

- sonstige Gebäude mit einer Höhe bis zu 7 m -

>> Sonderbau <<

Begründung:

- **Höhe des fertigen Fußbodens** im obersten Geschoss, in dem Aufenthaltsräume möglich sind, liegt gem. Bauantrag vom 17.07.2018 im Gebäude **im Mittel unter 7m.**
- Im Gesamtgebäude befindet sich neben den hier betrachteten zwei Büroeinheiten auch eine ambulant betreute Wohngemeinschaft. Es sind **mehr** als **zwei Nutzungseinheiten vorhanden.**
- **Sonderbau** nach Art. 2 Abs. 4 BayBO: **„Intensivpflege" und „sonstige Einrichtungen zur Unterbringung von Personen sowie Wohnheime"** (s. BSN 2014, Kreiter Thomas)

Beurteilungsgrundlage für die Einstufung des Gebäudes ist die **Bayerische Bauordnung.**

2.2 ANWENDBARE SONDERBAUVORSCHRIFTEN

Aufgrund der ausschließlichen Nutzung als Büro wird der hier betrachtete Bereich auf Grundlage der Bayerische Bauordnung bewertet.

2.3 PRÜFUNG DES BRANDSCHUTZNACHWEISES

Nach Art. 62b Abs. 2 BayBO benötigen Sonderbauten **eine vollumfängliche Prüfung** des vorliegenden Brandschutznachweises durch das zuständige Bauordnungsamt oder einen Prüfsachverständigen für Brandschutz.

Die beantragten Abweichungen sind genehmigungspflichtig und müssen geprüft werden.

Abweichungen sind vom Bauherrn zu beantragen und gelten nur dann als bewilligt, wenn sie im Genehmigungsbescheid zum Bauvorhaben ausdrücklich zugelassen werden.

2.4 BAUART UND -PRODUKTE

Allgemein ist auf die Anwendung der Art. 15 BayBO bis einschließlich Art. 23 BayBO (Bauprodukte und Bauarten) zu achten.

2.5 WEITERE VORSCHRIFTEN UND RICHTLINIEN

Für das Bauvorhaben sind weitere, wesentliche Vorschriften und Richtlinien einzuhalten. Hierbei sind insbesondere folgende Vorschriften in der aktuell gültigen Fassung zu berücksichtigen:

- BauVorlV: *Bauvorlagenverordnung*
- BayTB: *Bayerische Technische Baubestimmungen*

- DIN 4102: *Brandverhalten von Baustoffen und Bauteilen*
- DIN EN 13501: *Klassifizierung von Bauprodukten und Bauarten zu ihrem Brandverhalten*
- LAR: *Richtlinie über die brandschutztechnischen Anforderungen an Leitungsanlagen*
- LüAR: *Richtlinie über die brandschutztechnischen Anforderungen an Lüftungsanlagen*
- SPrüfV: *Verordnung über Prüfungen von sicherheitstechnischen Anlagen und Einrichtungen*

3 ABWEHRENDER BRANDSCHUTZ

3.1 FLÄCHEN FÜR DIE FEUERWEHR

Art. 5 BayBO

(1) [1]Von öffentlichen Verkehrsflächen ist insbesondere für die Feuerwehr ein geradliniger Zu- oder Durchgang zu rückwärtigen Gebäuden zu schaffen; zu anderen Gebäuden ist er zu schaffen, wenn der zweite Rettungsweg dieser Gebäude über Rettungsgeräte der Feuerwehr führt. [2]Zu Gebäuden, bei denen die Oberkante der Brüstung von zum Anleitern bestimmten Fenstern oder Stellen mehr als 8 m über dem Gelände liegt, ist in den Fällen des Satzes 1 an Stelle eines Zu- oder Durchgangs eine Zu- oder Durchfahrt zu schaffen. [3]Ist für die Personenrettung der Einsatz von Hubrettungsfahrzeugen erforderlich, sind die dafür erforderlichen Aufstell- und Bewegungsflächen vorzusehen. [4]Bei Gebäuden, die ganz oder mit Teilen mehr als 50 m von einer öffentlichen Verkehrsfläche entfernt sind, sind Zufahrten oder Durchfahrten nach Satz 2 zu den vor und hinter den Gebäuden gelegenen Grundstücksteilen und Bewegungsflächen herzustellen, wenn sie aus Gründen des Feuerwehreinsatzes erforderlich sind.

(2) [1]Zu- und Durchfahrten, Aufstellflächen und Bewegungsflächen müssen für Feuerwehreinsatzfahrzeuge ausreichend befestigt und tragfähig sein; sie sind als solche zu kennzeichnen und ständig frei zu halten; die Kennzeichnung von Zufahrten muss von der öffentlichen Verkehrsfläche aus sichtbar sein. [2]Fahrzeuge dürfen auf den Flächen nach Satz 1 nicht abgestellt werden.

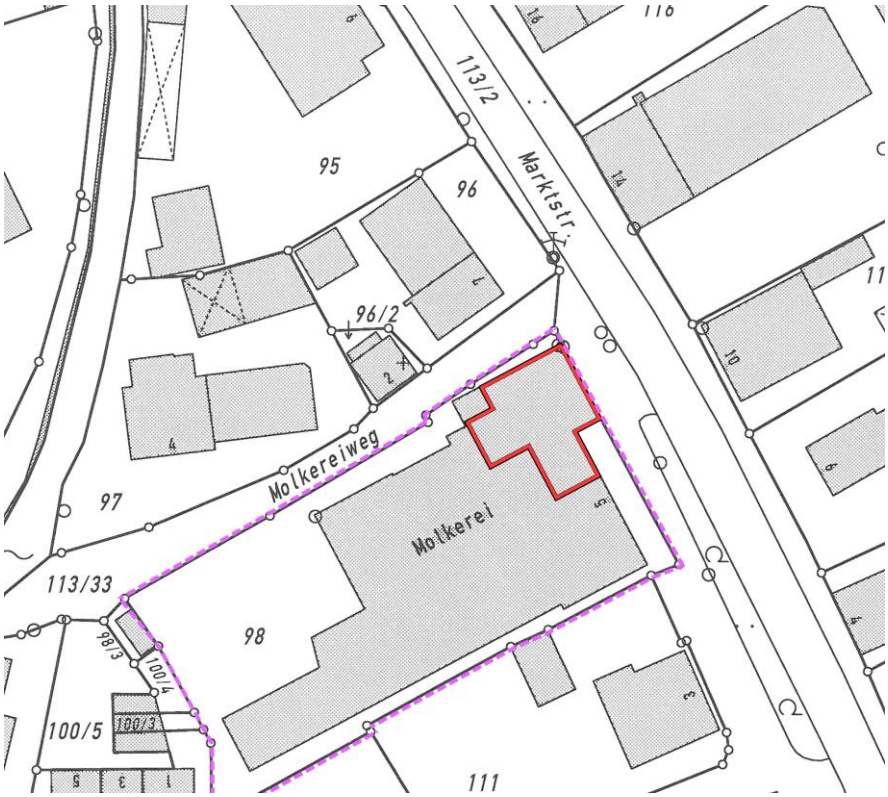

Abbildung 4: Lageplan - Feuerwehranfahrt

Das hier betrachtete Objekt ist für die Feuerwehr über die Marktstraße anfahrbar und zugänglich. Da aufgrund der Nutzungsänderung keine Änderungen an den äußeren Umfassungen des Bestandes vorgenommen werden wird die vorhandene Feuerwehranfahrt nicht verändert.

Der zweite Rettungsweg aus der Büroeinheit 1 muss aufgrund der Höhe über Gelände > 1,20 m über Rettungsgeräte der Feuerwehr (tragbare Leiter) geführt werden. Es ist ein Zu- oder Durchgang zu der Anleiterstelle auf der Ostseite gemäß den Richtlinien über Flächen für die Feuerwehr sicherzustellen:

- Geradlinig und mind. 1,25 m breit
- Für Türöffnungen und andere geringfügige Einengungen in diesen Zu- oder Durchgängen genügt eine lichte Breite von 1 m

3.2 ABSTANDSFLÄCHEN UND BRANDSCHUTZABSTÄNDE

Die notwendigen Abstandsflächen nach Art. 6 BayBO sind vom Entwurfsverfasser zu prüfen und nachzuweisen. Brandschutztechnische Bewertungen zu Abweichungen von Art. 6 sind dem Nachweisersteller nicht vorgelegt worden und sind deshalb nicht Teil des Brandschutznachweises. Diese sind vom Architekten separat zu beantragen.

Die brandschutzrelevanten Abstände zu den Nachbargrundstücken werden für das Gebäude unter dem Punkt 4.1 bewertet.

3.3 LÖSCHWASSERVERSORGUNG

Aufgrund der hier betrachteten Nutzungsänderung zu zwei Büroeinheiten wird die für den Bestand genehmigte Löschwassermenge nicht verändert. Aufgrund der Nutzungsänderung ergibt sich kein erhöhter Löschwasserbedarf.

3.4 RAUCHABLEITUNG

3.4.1. KELLER

Art. 35 BayBO

(3) [1]Jedes Kellergeschoss ohne Fenster muss mindestens eine Öffnung ins Freie haben, um eine Rauchableitung zu ermöglichen. [2]Gemeinsame Kellerlichtschächte für übereinander liegende Kellergeschosse sind unzulässig.

In dem hier betrachteten Kellerbereich sind keine Fenster (Lichtschächte) zur Rauchableitung vorhanden. Die Rauchableitung wird über den Nord-Westlichen Bereich (außerhalb Beurteilungsbereich) ermöglicht.

Aufgrund der unveränderten baulichen Bestandssituation im Kellergeschoss wird von einer genehmigten Bestandssituation bezüglich der Rauchableitung ausgegangen. In dem benachbarten Kellerbereich sind gemäß Grundrissplan „Bestand" Öffnungen zur Rauchableitung vorhanden.

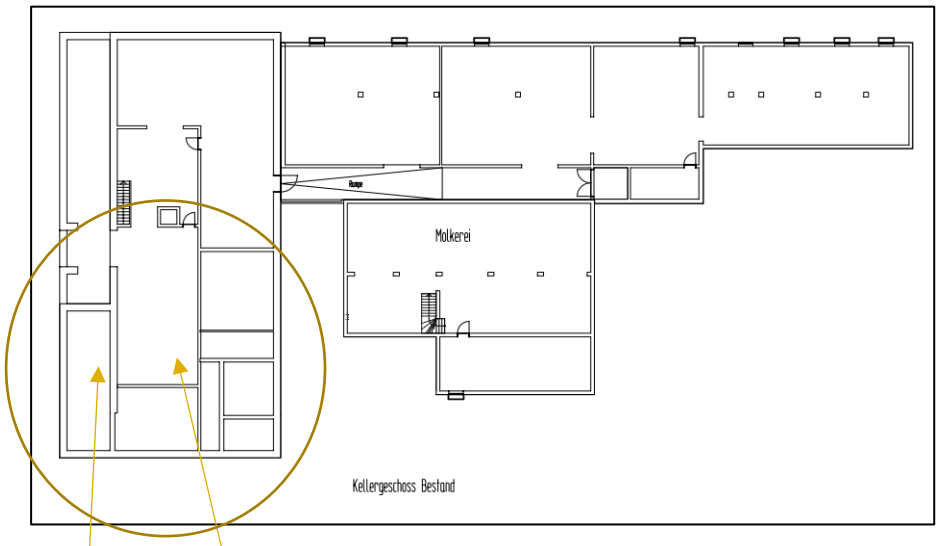

Abbildung 5: Grundriss Kellergeschoss

Neue Treppe | Einbau WCs

An die Rauchableitung aus den Obergeschossen werden im Standardbau keine Anforderungen gestellt. Die Rauchableitung kann jedoch über Fenster und Türen vorgenommen werden.

3.4.2. NOTWENDIGER TREPPENRAUM

Es ist kein notwendiger Treppenraum im Betrachtungsbereich vorhanden.

3.4.3. AUFZUG

Es ist kein Aufzug im Betrachtungsbereich vorhanden.

4 BAULICHER BRANDSCHUTZ

(vorbeugender Brandschutz)

4.1 BRANDABSCHNITTE, BRANDWÄNDE

Art. 28 BayBO

(1) Brandwände müssen als raumabschließende Bauteile zum Abschluss von Gebäuden (Gebäudeabschlusswand) oder zur Unterteilung von Gebäuden in Brandabschnitte (innere Brandwand) ausreichend lang die Brandausbreitung auf andere Gebäude oder Brandabschnitte verhindern.

Brandwände sind als raumabschließende Bauteile erforderlich zum Abschluss von Gebäuden (Gebäudeabschlusswand) oder zur Unterteilung von Gebäuden in Brandabschnitte (innere Brandwand).

Gebäudeabschlusswand

Art. 28 BayBO

(2) Brandwände sind erforderlich

1. als Gebäudeabschlusswand, ausgenommen von Gebäuden ohne Aufenthaltsräume und ohne Feuerstätten mit nicht mehr als 50 m³ Brutto-Rauminhalt, wenn diese Abschlusswände an oder mit einem Abstand bis zu 2,50 m gegenüber der Grundstücksgrenze errichtet werden, es sei denn, dass ein Abstand von mindestens 5 m zu bestehenden oder nach den baurechtlichen Vorschriften zulässigen künftigen Gebäuden gesichert ist, […]

Im Zuge der Nutzungsänderung sollen neue Fenster Richtung Norden und Osten eingebaut werden, sodass die Belange einer Gebäudeabschlusswand neu geprüft werden.

Der Abstand der nördlichen Außenwände des Gebäudes beträgt zu den Grundstücksgrenzen weniger als 2,50 m. Durch die öffentlichen Verkehrsflächen ist jedoch ein Abstand von 5 m zu zulässigen zukünftigen Gebäuden gesichert. Es ist keine Brandwand als Gebäudeabschlusswand erforderlich.

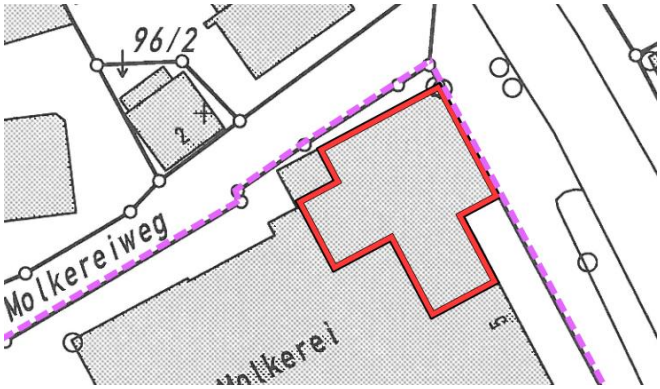

Abbildung 6: Auszug Lageplan mit Grundstücksgrenze

Innere Brandwände

Art. 28 BayBO

(2) Brandwände sind erforderlich […]

2. als innere Brandwand zur Unterteilung ausgedehnter Gebäude in Abständen von nicht mehr als 40 m, […]

Durch die Nutzungsänderung wird das Bestandsgebäude nicht in seiner Ausdehnung verändert, sodass eine genehmigte Bestandssituation bezüglich der Brandabschnittstrennung angenommen wird. Gemäß Brandschutzkonzept von 2014 (Thomas Kreiter) ist in dem hier betrachteten Bereich keine Brandabschnittstrennung vorhanden.

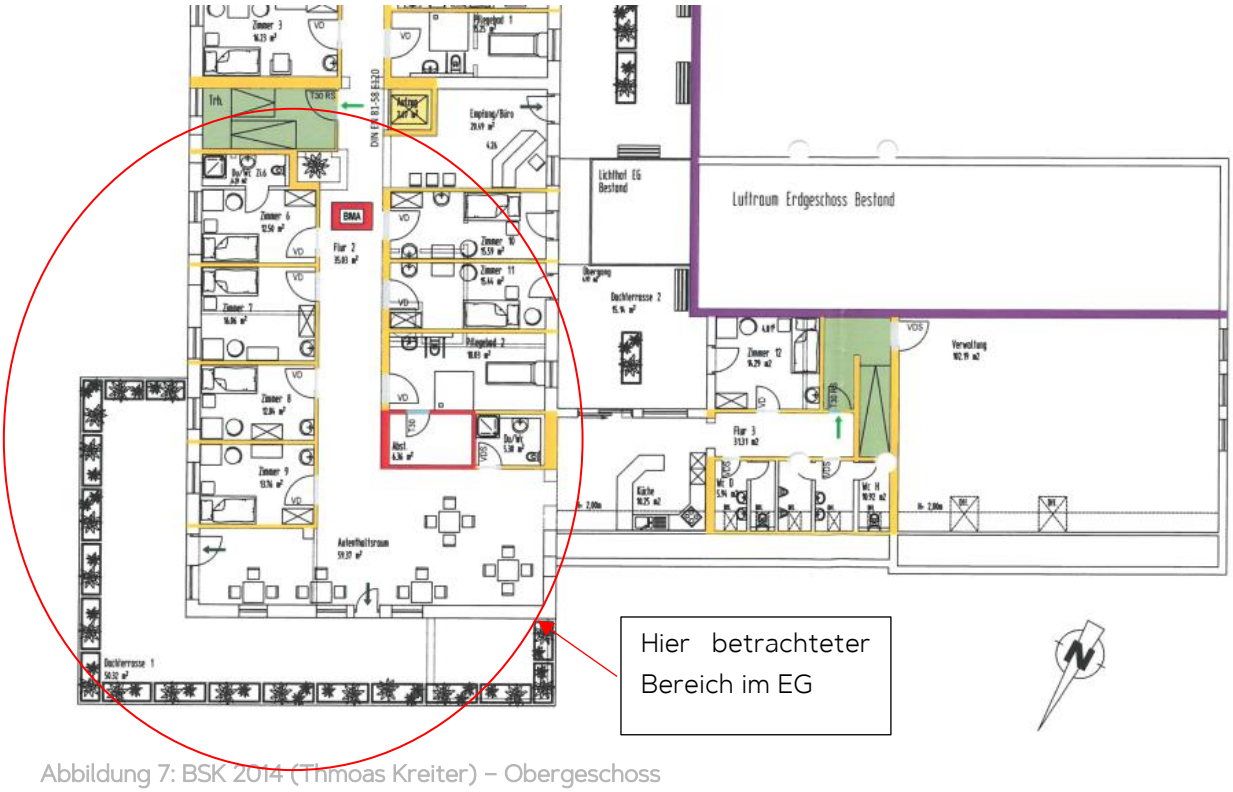

Abbildung 7: BSK 2014 (Thmoas Kreiter) – Obergeschoss

4.2 ANFORDERUNGEN AN WESENTLICHE BAUTEILE

4.2.1. TRAGENDE UND AUSSTEIFENDE WÄNDE UND STÜTZEN

Kellergeschoss

Art. 25 BayBO

(2) Im Kellergeschoss müssen tragende und aussteifende Wände und Stützen

1. in Gebäuden der Gebäudeklassen 3 bis 5 feuerbeständig sein

Die tragenden und aussteifenden Wände und Stützen im Kellergeschoss müssen feuerbeständig ausgeführt sein. Eine Bauteilüberprüfung findet nicht statt. Es wird eine genehmigte Bestandssituation der massiven Konstruktion angenommen.

Oberirdische Geschosse

Art. 25 BayBO

(1) [1]Tragende und aussteifende Wände und Stützen müssen im Brandfall ausreichend lang standsicher sein. [2]Sie müssen […]

3. in Gebäuden der Gebäudeklassen 2 und 3 feuerhemmend sein.

[3]Satz 2 gilt

1. für Geschosse im Dachraum nur, wenn darüber noch Aufenthaltsräume möglich sind; Art. 27 Abs. 4 bleibt unberührt,

2. nicht für Balkone, ausgenommen offene Gänge, die als notwendige Flure dienen.

Die tragenden und aussteifenden Wände und Stützen müssen in den oberirdischen Geschossen feuerhemmend ausgeführt sein. Eine Bauteilüberprüfung findet nicht statt. Es wird eine genehmigte Bestandssituation der massiven Konstruktion angenommen.

4.2.2. DECKEN

Kellergeschoss

Art. 29 BayBO

(1) [1]Decken müssen als tragende und raumabschließende Bauteile zwischen Geschossen im Brandfall ausreichend lang standsicher und widerstandsfähig gegen die Brandausbreitung sein. […]

(2) [1]Im Kellergeschoss müssen Decken

1. in Gebäuden der Gebäudeklassen 3 bis 5 feuerbeständig sein

[2]Decken müssen feuerbeständig sein

1. unter und über Räumen mit Explosions- oder erhöhter Brandgefahr, ausgenommen in Wohngebäuden der Gebäudeklassen 1 und 2,

2. zwischen dem landwirtschaftlich genutzten Teil und dem Wohnteil eines Gebäudes.

(3) Der Anschluss der Decken an die Außenwand ist so herzustellen, dass er den Anforderungen aus Abs. 1 Satz 1 genügt.

Die Decke über dem Kellergeschoss muss als tragendes und raumabschließendes Bauteil feuerbeständig ausgeführt sein. Eine Bauteilüberprüfung findet nicht statt. Es wird eine genehmigte Bestandssituation der massiven Stahlbetondecken (s. BSN 2014) angenommen. Der Anschluss der Decke an die Außenwand muss so ausgebildet sein, dass die Anforderungen an die Tragfähigkeit und die Feuerwiderstandsfähigkeit im Brandfall erfüllt sind.

Oberirdische Geschosse

Art. 29 BayBO

(1) [1]Decken müssen als tragende und raumabschließende Bauteile zwischen Geschossen im Brandfall ausreichend lang standsicher und widerstandsfähig gegen die Brandausbreitung sein. [2]Sie müssen […]

3. in Gebäuden der Gebäudeklasse 3 feuerhemmend sein.

[3]Satz 2 gilt

1. für Geschosse im Dachraum nur, wenn darüber Aufenthaltsräume möglich sind; Art. 27 Abs. 4 bleibt unberührt,

2. nicht für Balkone, ausgenommen offene Gänge, die als notwendige Flure dienen.

(3) Der Anschluss der Decken an die Außenwand ist so herzustellen, dass er den Anforderungen aus Abs. 1 Satz 1 genügt.

Die Decken über dem hier betrachteten erdgeschossigen Bereich muss als tragende und raumabschließende Bauteile feuerhemmend ausgeführt sein. Eine Bauteilüberprüfung findet nicht statt. Es wird eine genehmigte Bestandssituation der massiven Stahlbetondecken (s. BSN 2014) angenommen. Der Anschluss der Decken an die Außenwand muss so ausgebildet sein, dass die Anforderungen an die Feuerwiderstandsfähigkeit und den Raumabschluss im Brandfall erfüllt sind.

Öffnungen in Decken

Art. 29 BayBO

(4) Öffnungen in Decken, für die eine Feuerwiderstandsfähigkeit vorgeschrieben ist, sind nur zulässig

1. in Gebäuden der Gebäudeklasse 1 und 2,

2. innerhalb derselben Nutzungseinheit mit insgesamt nicht mehr als 400 m² in nicht mehr als zwei Geschossen,

3. im Übrigen, wenn sie auf die für die Nutzung erforderliche Zahl und Größe beschränkt sind und Abschlüsse mit der Feuerwiderstandsfähigkeit der Decke haben.

In der kleineren Büroeinheit 1 ist eine Öffnung in der Decke zum Kellergeschoss vorhanden. Die Öffnung wird im Kellergeschoss zu den restlichen Lagerräumen des Gebäudes feuerbeständig und mit feuerhemmender, dichter- und selbstschließender Tür (siehe Kapitel 4.2.4) abgetrennt, sodass eine Fläche von ca. 120 m² EG und OG zusammenhängen.

4.2.3. AUßENWÄNDE

Art. 26 BayBO

(1) Außenwände und Außenwandteile wie Brüstungen und Schürzen sind so auszubilden, dass eine Brandausbreitung auf und in diesen Bauteilen ausreichend lang begrenzt ist.

(2) [1] Nichttragende Außenwände und nichttragende Teile tragender Außenwände müssen aus nichtbrennbaren Baustoffen bestehen; sie sind aus brennbaren Baustoffen zulässig, wenn sie als raumabschließende Bauteile feuerhemmend sind. [2] Satz 1 gilt nicht für

1. Fenster und Türen,

2. Fugendichtungen und

3. brennbare Dämmstoffe in nichtbrennbaren geschlossenen Profilen der Außenwand-konstruktion.

(3) [1] Oberflächen von Außenwänden sowie Außenwandbekleidungen müssen einschließlich der Dämmstoffe und Unterkonstruktionen schwerentflammbar sein; Unterkonstruktionen aus normalentflammbaren Baustoffen sind zulässig, wenn die Anforderungen nach Abs. 1 erfüllt sind. [2] Balkonbekleidungen, die über die erforderliche Umwehrungshöhe hinaus hochgeführt werden, und mehr als zwei Geschosse überbrückende Solaranlagen an Außenwänden müssen schwerentflammbar sein. [3] Baustoffe, die schwerentflammbar sein müssen, in Bauteilen nach Satz 1 Halbsatz 1 und Satz 2 dürfen nicht brennend abfallen oder abtropfen.

(4) Bei Außenwandkonstruktionen mit geschossübergreifenden Hohl- oder Lufträumen wie Doppelfassaden sind gegen die Brandausbreitung besondere Vorkehrungen zu treffen; das gilt für hinterlüftete Außenwandbekleidungen entsprechend.

(5) Die Abs. 2,3 und 4 Halbsatz 2 gelten nicht für Gebäude der Gebäudeklassen 1 bis 3, Abs. 4 Halbsatz 1 nicht für Gebäude der Gebäudeklassen 1 und 2.

An den im Bestand vorhandenen Außenwänden (Mauerwerk verputzt) finden keine Änderungen/ Eingriffe statt, sodass genehmigter Bestand der Außenwand geltend gemacht werden kann.

4.2.4. TRENNWÄNDE

Art. 27 BayBO

(1) Trennwände nach Abs. 2 müssen als raumabschließende Bauteile von Räumen oder Nutzungseinheiten innerhalb von Geschossen ausreichend lang widerstandsfähig gegen die Brandausbreitung sein.

(2) Trennwände sind erforderlich

1. zwischen Nutzungseinheiten sowie zwischen Nutzungseinheiten und anders genutzten Räumen, ausgenommen notwendigen Fluren,

2. zum Abschluss von Räumen mit Explosions- oder erhöhter Brandgefahr,

3. zwischen Aufenthaltsräumen und anders genutzten Räumen im Kellergeschoss.

(3) [1] Trennwände nach Abs. 2 Nrn. 1 und 3 müssen die Feuerwiderstandsfähigkeit der tragenden und aussteifenden Bauteile des Geschosses haben, jedoch mindestens feuerhemmend sein. [2] Trennwände nach Abs. 2 Nr. 2 müssen feuerbeständig sein.

Der Verlauf der bauordnungsrechtlich erforderlichen Trennwände ist nachstehend beschrieben und dargestellt:

Zwischen den beiden Büroeinheiten sowie zur angrenzenden Bestandsnutzung ist eine feuerhemmende Trennwand erforderlich. Im Kellergeschoss wird zur Schließung der Deckenöffnung eine feuerbeständige Wand gefordert.

Anschluss der Trennwände

Art. 27 BayBO

(4) Die Trennwände nach Abs. 2 sind bis zur Rohdecke, im Dachraum bis unter die Dachhaut zu führen; werden in Dachräumen Trennwände nur bis zur Rohdecke geführt, ist diese Decke als raumabschließendes Bauteil einschließlich der sie tragenden und aussteifenden Bauteile feuerhemmend herzustellen.

Die Trennwände sind bis zur Rohdecke zu führen.

Öffnungen in Trennwänden

Art. 27 BayBO

(5) Öffnungen in Trennwänden nach Abs. 2 sind nur zulässig, wenn sie auf die für die Nutzung erforderliche Zahl und Größe beschränkt sind; sie müssen feuerhemmende, dicht- und selbstschließende Abschlüsse haben.

Die Öffnung in der Trennwand im Kellergeschoss muss feuerhemmend, dicht- und selbstschließend sein.

Räumen mit Explosions- oder erhöhter Brandgefahr

Räume mit explosions- oder erhöhter Brandgefahr sind im hier betrachteten Bereich nicht vorhanden

Räume mit anderer Nutzung

Räume, die keiner der hier betrachteten Nutzungseinheiten zugehören sind innerhalb des Betrachtungsbereichs nicht vorhanden.

4.2.5. DÄCHER

Art. 30 BayBO

(1) Bedachungen müssen gegen eine Brandbeanspruchung von außen durch Flugfeuer und strahlende Wärme ausreichend lang widerstandsfähig sein (harte Bedachung).

Im Zuge der hier betrachteten Nutzungsänderung finden keine Eingriffe in das Bestandsdach statt sodass genehmigter Bestand geltend gemacht wird.

Dächer von Anbauten

Art. 30 BayBO

(7) [1]Dächer von Anbauten, die an Außenwände mit Öffnungen oder ohne Feuerwiderstandsfähigkeit anschließen, müssen innerhalb eines Abstands von 5 m von diesen Wänden als raumabschließende Bauteile für eine Brandbeanspruchung von innen nach außen einschließlich der sie tragenden und aussteifenden Bauteile die Feuerwiderstandsfähigkeit der Decken des Gebäudeteils haben, an den sie angebaut werden. [2]Das gilt nicht für Anbauten an Wohngebäude der Gebäudeklassen 1 bis 3.

Der hier betrachtete Bereich stellt ein Anbaudach dar, das in einem Abstand von 5 m zur aufgehenden Fassade einschließlich der sie tragenden und aussteifenden Bauteile als raumabschließendes Bauteil von unten feuerhemmend sein muss. Aufgrund der Nutzungsänderung finden keine Änderungen dieses Daches statt, sodass eine genehmigte Bestandsituation angenommen werden kann.

Abbildung 8: Ansicht Ost - Dächer von Anbauten

4.3 RETTUNGSWEGE

4.3.1. ANZAHL, VERLAUF UND AUSGÄNGE

Art. 31 BayBO

(1) Für Nutzungseinheiten mit mindestens einem Aufenthaltsraum wie Wohnungen, Praxen, selbstständige Betriebsstätten müssen in jedem Geschoss mindestens zwei voneinander unabhängige Rettungswege ins Freie vorhanden sein; beide Rettungswege dürfen jedoch innerhalb des Geschosses über denselben notwendigen Flur führen.

(2) [1] Für Nutzungseinheiten nach Abs. 1, die nicht zu ebener Erde liegen, muss der erste Rettungsweg über eine notwendige Treppe führen. [2]Der zweite Rettungsweg kann eine weitere notwendige Treppe oder eine mit Rettungsgeräten der Feuerwehr erreichbare Stelle der Nutzungseinheit sein. [3]Ein zweiter Rettungsweg ist nicht erforderlich, wenn die Rettung über einen sicher erreichbaren Treppenraum möglich ist, in den Feuer und Rauch nicht eindringen können (Sicherheitstreppenraum).

Art. 33 BayBO

(2) [2] Übereinanderliegende Kellergeschosse müssen jeweils mindestens zwei Ausgänge in notwendige Treppenräume oder ins Freie haben.

Für Nutzungseinheiten mit mindestens einem Aufenthaltsraum müssen in jedem Geschoss mindestens zwei voneinander unabhängige Rettungswege vorhanden sein. Nachfolgend wird der Verlauf der Rettungswege in den einzelnen Geschossen bzw. Nutzungseinheiten beschrieben:

Büroeinheit 1

Für die Büroeinheit steht ein direkter Ausgang ins Freie im Erdgeschoss zur Verfügung. Der zweite Rettungsweg kann über ein Fenster mit Anleiterung durch Rettungsgeräte der Feuerwehr (Steckleiter) ermöglicht werden. Für den Lagerraum im Kellergeschoss sowie für die zur Büroeinheiten dazugehörigen WCs führt der Rettungsweg über die interne notwendige Treppe ins Erdgeschoss. Ein weitere Rettungsweg ist für den Lagerraum/WC-Bereich im Kellergeschoss nicht nachzuweisen. Ein Aufenthaltsraum ist im hier betrachteten Bereich nicht vorhanden.

Kellergeschoss

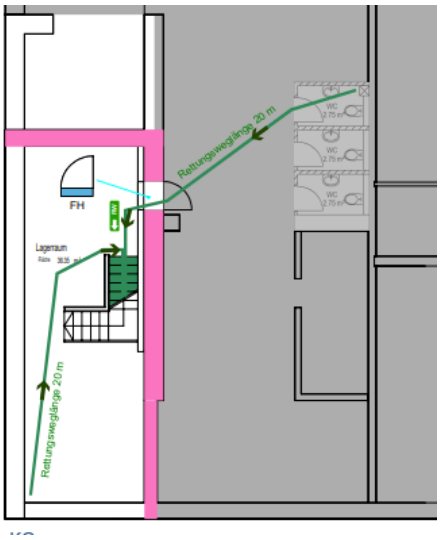

Abbildung 9: Rettungsweg KG Büro 1

Abbildung 10: RW-Führung Kellergeschoss

Büroeinheit 183 m²:

Die Büroeinheit hat einen Ausgang auf den notwendigen Flur. Im weiteren Verlauf wird der Ausgang ins Freie erreicht. Der zweite Rettungsweg wird über ein Fensterausstieg (Selbstrettung) ermöglicht.

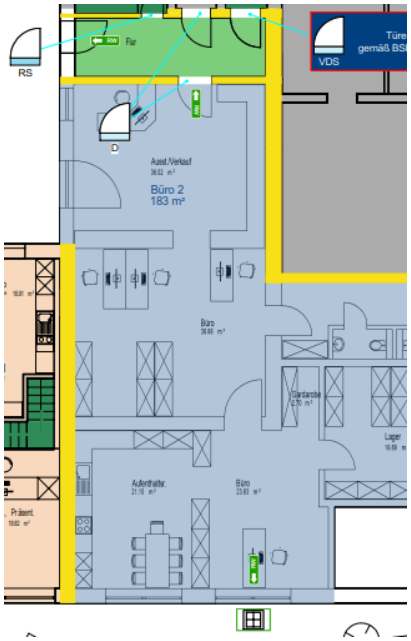

Abbildung 11: RW-Führung Erdgeschoss

4.3.2. RETTUNGSWEGLÄNGEN

Art. 33 BayBO

(2) [1]Von jeder Stelle eines Aufenthaltsraums sowie eines Kellergeschosses muss mindestens ein Ausgang in einen notwendigen Treppenraum oder ins Freie in höchstens 35 m Entfernung erreichbar sein; das gilt nicht für land- oder forstwirtschaftliche Gebäude. […]

Die maximal zulässige Rettungsweglänge von 35 m bis zu einem Ausgang ins Freie oder zum notwendigen Treppenraum ist von jeder Stelle der Büroeinheiten sowie des Kellergeschosses (gemessen an den hier betrachteten WCs) eingehalten.

4.3.3. RETTUNGSWEGBREITEN

Art. 32 BayBO

(5) Die nutzbare Breite der Treppenläufe und Treppenabsätze notwendiger Treppen muss für den größten zu erwartenden Verkehr ausreichen.

Art. 34 BayBO

(2) [1]Notwendige Flure müssen so breit sein, dass sie für den größten zu erwartenden Verkehr ausreichen. […]

Aus brandschutztechnischer Sicht bestehen über die bauordnungsrechtlichen Anforderungen hinaus keine Mindestanforderungen an die Mindestbreite von Rettungswegen, diese müssen für den größten zu erwartenden Verkehr ausreichen. Es wird jedoch darauf hingewiesen, dass sich z.B. aus der DIN 18065 weitergehende Anforderungen an die Mindestbreite von Treppen ergeben können. Diese ist als technische Baubestimmung in Bayern bauordnungsrechtlich eingeführt und zwingend einzuhalten.

Da es sich darüber hinaus um eine Arbeitsstätte handelt, wird darauf hingewiesen, dass sich aus dem geltenden Arbeitsstättenrecht weitergehende Anforderungen diesbezüglich ergeben können. Eine Überprüfung dieser Anforderungen ist nach § 11 BauVorlV nicht Teil des bauordnungsrechtlichen Brandschutznachweises.

4.3.4. NOTWENDIGE TREPPEN

Art. 32 BayBO

(1) [1]Jedes nicht zu ebener Erde liegende Geschoss und der benutzbare Dachraum eines Gebäudes müssen über mindestens eine Treppe zugänglich sein (notwendige Treppe). [2]Statt notwendiger Treppen sind Rampen mit flacher Neigung zulässig.

(2) [1]Einschiebbare Treppen und Rolltreppen sind als notwendige Treppen unzulässig. [2]In Gebäuden der Gebäudeklassen 1 und 2 sind einschiebbare Treppen und Leitern als Zugang zu einem Dachraum ohne Aufenthaltsraum zulässig.

(3) [1]Notwendige Treppen sind in einem Zuge zu allen angeschlossenen Geschossen zu führen; sie müssen mit den Treppen zum Dachraum unmittelbar verbunden sein. [2]Das gilt nicht für Treppen

1. in Gebäuden der Gebäudeklassen 1 bis 3,

2. nach Art. 33 Abs. 1 Satz 3 Nr. 2.

(4) [1]Die tragenden Teile notwendiger Treppen müssen […]

3. in Gebäuden der Gebäudeklasse 3 aus nichtbrennbaren Baustoffen oder feuerhemmend sein. [2]Tragende Teile von Außentreppen nach Art. 33 Abs. 1 Satz 3 Nr. 3 für Gebäude der Gebäudeklassen 3 bis 5 müssen aus nichtbrennbaren Baustoffen bestehen.

(6) [1]Treppen müssen einen festen und griffsicheren Handlauf haben. [2]Für Treppen sind Handläufe auf beiden Seiten und Zwischenhandläufe vorzusehen, soweit die Verkehrssicherheit dies erfordert.

Die tragenden Teile der notwendigen Treppen innerhalb der Büroeinheit „Büro 1" müssen feuerhemmend oder aus nichtbrennbaren Baustoffen ausgeführt werden. Die Treppe wird in Stahlbeton errichtet und erfüllt damit die o.g. Anforderungen.

4.3.5. NOTWENDIGE TREPPENRÄUME

Art. 33 BayBO

(1) [1]Jede notwendige Treppe muss zur Sicherung der Rettungswege aus den Geschossen ins Freie in einem eigenen, durchgehenden Treppenraum liegen (notwendiger Treppenraum). [2]Notwendige Treppenräume müssen so angeordnet und ausgebildet sein, dass die Nutzung der notwendigen Treppen im Brandfall ausreichend lang möglich ist. [3]Notwendige Treppen sind ohne eigenen Treppenraum zulässig

1. in Gebäuden der Gebäudeklassen 1 und 2,

2. für die Verbindung von höchstens zwei Geschossen innerhalb derselben Nutzungseinheit von insgesamt nicht mehr als 200 m2, wenn in jedem Geschoss ein anderer Rettungsweg erreicht werden kann,

3. als Außentreppe, wenn ihre Nutzung ausreichend sicher ist und im Brandfall nicht gefährdet werden kann.

Die notwendige Treppe im hier betrachteten Bereich „Büro 1" soll ohne eigenen notwendigen Treppenraum errichtet werden. Die hier betrachtete offene Treppe erstreckt sich über zwei Geschosse mit einer Brutto-Grundfläche von ca. 120 m². Für den fehlenden weiteren Rettungsweg aus dem

Kellergeschoss gem. Art. 33 (1) Nr. 2 BayBO wird eine Abweichung beantragt. Aus brandschutztechnischer Sicht kann die Abweichung akzeptiert werden, da es sich bei den hier betrachteten Räumen im Kellergeschoss (Lagerraum und WC) um keine Aufenthaltsräume handelt und auch keine Aufenthaltsräume zulässig sind.

Der feuerhemmend abgetrennte notwendige Treppenraum im Bestand liegt außerhalb des Betrachtungsbereichs. Dieser wurde gem. BSN 2014 bewertet. Die gemäß BSN 2014 nicht bewerteten Türen am Treppenraum, welche an die hier betrachtete Nutzungsänderung angrenzen werden im Zuge dieses Brandschutznachweises definiert (siehe Kapitel 4.3.6).

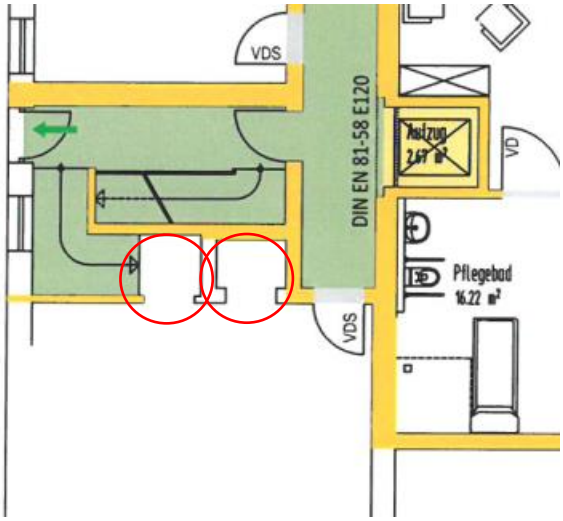

Abbildung 12: Auszug BSK 2014 (Thmomas Kreiter) - Treppenraum Erdgeschoss

4.3.6. NOTWENDIGE FLURE

Art. 34 BayBO

(1) [1]Flure, über die Rettungswege aus Aufenthaltsräumen oder aus Nutzungseinheiten mit Aufenthaltsräumen zu Ausgängen in notwendige Treppenräume oder ins Freie führen (notwendige Flure), müssen so angeordnet und ausgebildet sein, dass die Nutzung im Brandfall ausreichend lang möglich ist. [2]Notwendige Flure sind nicht erforderlich

1. in Wohngebäuden der Gebäudeklassen 1 und 2,

2. in sonstigen Gebäuden der Gebäudeklassen 1 und 2, ausgenommen in Kellergeschossen,

3. innerhalb von Wohnungen oder innerhalb von Nutzungseinheiten mit nicht mehr als 200 m²,

4. innerhalb von Nutzungseinheiten, die einer Büro- oder Verwaltungsnutzung dienen, mit nicht mehr als 400 m²; das gilt auch für Teile größerer Nutzungseinheiten, wenn diese Teile nicht größer als 400 m² sind, Trennwände nach Art. 27 Abs. 2 Nr. 1 haben und jeder Teil unabhängig von anderen Teilen Rettungswege nach Art. 31 Abs. 1 hat.

Flure, über die Rettungswege aus Aufenthaltsräumen oder Nutzungseinheiten mit Aufenthaltsräumen zu Ausgängen in notwendige Treppenräume oder ins Freie geführt werden, müssen als notwendige Flure ausgebildet werden.

Für die Büroeinheit 2 wird der Rettungsweg über einen notwendigen Flur ins Freie geführt. Da der Brandschutznachweis von 2014 diesen Flur nicht mitbewertet hat (siehe Abbildung 12) , werden die erforderlichen Anforderungen an einen notwendigen Flur nachfolgend definiert:

Wände

Art. 34 BayBO

(4) [1]Die Wände notwendiger Flure müssen als raumabschließende Bauteile feuerhemmend, in Kellergeschossen, deren tragende und aussteifende Bauteile feuerbeständig sein müssen, feuerbeständig sein. [2]Die Wände sind bis an die Rohdecke zu führen. [3]Sie dürfen bis an die Unterdecke der Flure geführt werden, wenn die Unterdecke feuerhemmend und ein demjenigen nach Satz 1 vergleichbarer Raumabschluss sichergestellt ist.

(5) [1]Für Wände und Brüstungen notwendiger Flure mit nur einer Fluchtrichtung, die als offene Gänge vor den Außenwänden angeordnet sind, gilt Abs. 4 entsprechend. [2]Fenster sind in diesen Außenwänden ab einer Brüstungshöhe von 0,90 m zulässig.

Die Wände des notwendigen Flurs müssen in den oberirdischen Geschossen als raumabschließende Bauteile feuerhemmend ausgeführt werden. Die Wände sind grundsätzlich bis an die Rohdecke oder an eine feuerhemmende Unterdecke zu führen, wenn ein gleichwertiger Raumabschluss sichergestellt werden kann.

Öffnungen zum notwendigen Flur

Art. 34 BayBO

(4) […] 4Türen in diesen Wänden müssen dicht schließen; Öffnungen zu Lagerbereichen im Kellergeschoss müssen feuerhemmende, dicht- und selbstschließende Abschlüsse haben.

Türen in den Wänden notwendiger Flure müssen grundsätzlich dicht schließend ausgeführt werden.

Die gem. BSN 2014 geforderte vollwandige, dicht- und selbstschließende Tür zum Flur kann erhalten bleiben.

Die Tür zum Treppenraum ist gemäß Art. 33 (6) BayBO als rauchdichte und selbstschließende Tür auszuführen.

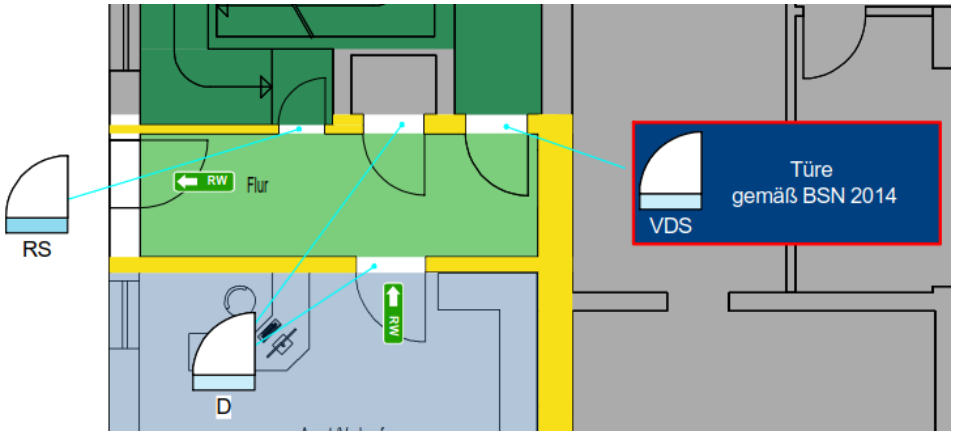

Abbildung 13: Auszug BSK 30.01.2019 - Erdgeschoss

Rauchabschnitte

Art. 34 BayBO

(3) 1Notwendige Flure sind durch nichtabschließbare, rauchdichte und selbstschließende

Abschlüsse in Rauchabschnitte zu unterteilen. [2]Die Rauchabschnitte sollen nicht länger als 30 m sein. [3]Die Abschlüsse sind bis an die Rohdecke zu führen; sie dürfen bis an die Unterdecke der Flure geführt werden, wenn die Unterdecke feuerhemmend ist.

Art. 34 BayBO

(3) [1]Notwendige Flure sind durch nichtabschließbare, rauchdichte und selbstschließende

Abschlüsse in Rauchabschnitte zu unterteilen. [2]Die Rauchabschnitte sollen nicht länger als 30 m sein. [3]Die Abschlüsse sind bis an die Rohdecke zu führen; sie dürfen bis an die Unterdecke der Flure geführt werden, wenn die Unterdecke feuerhemmend ist.

In dem hier betrachteten notwendigen Flur ist keine Unterteilung in Rauchabschnitte erforderlich.

Bekleidungen

Art. 34 BayBO

(6) In notwendigen Fluren sowie in offenen Gängen nach Abs. 5 müssen

1.Bekleidungen, Putze, Unterdecken und Dämmstoffe aus nichtbrennbaren Baustoffen bestehen,

2.Wände und Decken aus brennbaren Baustoffen eine Bekleidung aus nichtbrennbaren Baustoffen in ausreichender Dicke haben.

Bekleidungen, Putze, Unterdecken und Dämmstoffe in den notwendigen Fluren müssen aus nichtbrennbaren Baustoffen bestehen. Wände und Decken aus brennbaren Baustoffen müssen eine Bekleidung aus nichtbrennbaren Baustoffen in ausreichender Dicke haben.

4.3.7. RETTUNGSWEGE ÜBER FENSTER

Art. 35 BayBO

(4) [1]Fenster, die als Rettungswege nach Art. 31 Abs. 2 Satz 2 dienen, müssen in der Breite mindestens 0,60 m, in der Höhe mindestens 1,0 m groß, von innen zu öffnen und nicht höher als 1,20 m über der Fußbodenoberkante angeordnet sein. [2]Liegen diese Fenster in Dachschrägen oder Dachaufbauten, so darf ihre Unterkante oder ein davor liegender Austritt von der Traufkante horizontal gemessen nicht mehr als 1 m entfernt sein.

Das erdgeschossige Fenster der Büroeinheit 2, das zur Rettungswegführung (Selbstrettung) dient, muss die nachstehenden Anforderungen erfüllen:

- Mindestbreite 0,60 m (lichtes Durchgangsmaß)
- Mindesthöhe 1,0 m (lichtes Durchgangsmaß)
- Brüstungshöhe max. 1,20 m (innen und außen)
- von innen öffenbar

Das Fenster auf der Ostseite der Büroeinheit 1, das zur Rettungswegführung über Rettungsgeräte der Feuerwehr dient, muss die nachstehenden Anforderungen erfüllen:

- Mindestbreite 0,60 m (lichtes Durchgangsmaß)
- Mindesthöhe 1,0 m (lichtes Durchgangsmaß)
- Brüstungshöhe max. 1,20 m (innen)
- von innen öffenbar
- Die Anleiterung muss unter einem Anstellwinkel der Leiter von 68 ° - 75 ° möglich sein.

- Im Außenbereich muss darauf geachtet werden, dass die Leiter auf möglichst ebenem Gelände aufgestellt werden kann

4.3.8. TÜREN IN RETTUNGSWEGEN

Türen in Rettungswegen müssen sich leicht in voller Breite und ohne besondere Hilfsmittel öffnen lassen. Leicht zu öffnen bedeutet, dass die Öffnungseinrichtung gut erkennbar und an zugänglicher Stelle angebracht, sowie dass die Betätigungsart leicht verständlich und das Öffnen mit nur geringer Kraft möglich ist.

Sollen Zugänge vor unbefugter Benutzung geschützt werden, sind Fluchttürsteuergeräte mit Alarmüberwachung, Fluchttürwächter oder Panikbeschläge einzubauen.

Schlüsselkästen sind nicht zulässig.

Türen in Rettungswegen dürfen nur dann verschlossen werden, wenn Betriebszeiten definiert sind. Innerhalb dieser Betriebszeit muss vom Betreiber sichergestellt werden, dass diese Türen nicht verschlossen sind.

Selbstschließende Türen mit Anforderungen an den Brandschutz, die aus betrieblichen Gründen offengehalten werden, müssen mit Feststellanlagen versehen werden, die bei Raucheinwirkung ein selbsttätiges Schließen bewirken.

Hinsichtlich der Aufschlagrichtung der Türen werden bauordnungsrechtlich für das hier betrachtete Gebäude keine Aussagen getroffen. Es wird jedoch darauf hingewiesen, dass sich aus dem Arbeitsstättenrecht diesbezüglich weitergehende Anforderungen ergeben können. Eine Überprüfung und Definition dieser Anforderungen ist nicht Bestandteil des bauordnungsrechtlichen Brandschutznachweises.

Elektrische Verriegelungssysteme von Türen in Rettungswegen

Für elektrische Verriegelungen von Türen in Rettungswegen gelten die Anforderungen der Richtlinie über elektrische Verriegelungssysteme von Türen in Rettungswegen (EltVTR).

5 ANLAGENTECHNISCHER BRANDSCHUTZ

5.1 ALLGEMEINE TECHNISCHE GEBÄUDEAUSRÜSTUNG

5.1.1. AUFZUG

Im Betrachtungsbereich ist kein Aufzug vorhanden.

5.1.2. LEITUNGSANLAGEN SOWIE INSTALLATIONSSCHÄCHTE UND -KANÄLE

Art. 38 BayBO

(1) Leitungen dürfen durch raumabschließende Bauteile, für die eine Feuerwiderstandsfähigkeit vorgeschrieben ist, nur hindurchgeführt werden, wenn eine Brandausbreitung ausreichend lang nicht zu befürchten ist oder Vorkehrungen hiergegen getroffen sind; das gilt nicht

1. innerhalb von Gebäuden der Gebäudeklassen 1 und 2,

2. innerhalb von Wohnungen,

3. innerhalb derselben Nutzungseinheit mit insgesamt nicht mehr als 400 m² in nicht mehr als zwei Geschossen.

(2) In notwendigen Treppenräumen, in Räumen nach Art. 33 Abs. 3 Satz 2 und in notwendigen Fluren sind Leitungsanlagen nur zulässig, wenn eine Nutzung als Rettungsweg im Brandfall ausreichend lang möglich ist.

(3) Für Installationsschächte und -kanäle gelten Abs. 1 sowie Art. 39 Abs. 2 Satz 1 und Abs. 3 entsprechend

LAR

Bei der Verlegung von Leitungen wird auf die Leitungsanlagenrichtlinie (LAR) verwiesen. Die Leitungsanlagenrichtlinie ist vollumfänglich einzuhalten.

Die Richtlinie gilt für

- Leitungsanlagen in notwendigen Treppenräumen, in Räumen zwischen notwendigen Treppenräumen und Ausgängen ins Freie, in notwendigen Fluren ausgenommen in offenen Gängen vor Außenwänden,
- die Führung von Leitungen durch raumabschließend feuerwiderstandsfähige Bauteile (Wände und Decken),
- den Funktionserhalt von elektrischen Leitungsanlagen im Brandfall.

Für bauordnungsrechtlich vorgeschriebene Vorräume und Sicherheitsschleusen gilt die Richtlinie entsprechend. In diesen Räumen gelten die Anforderungen wie an notwendige Treppenräume.

Sie gilt nicht für Lüftungs- und Warmluftheizungsanlagen. Für Lüftungsanlagen ist die Musterrichtlinie über die brandschutztechnischen Anforderungen an Lüftungsanlagen (M-LüAR) zu beachten. Die Musterrichtlinie über brandschutztechnische Anforderungen an hochfeuerhemmende Bauteile in Holzbauweise (M-HFHHolzR) bleibt unberührt.

Leitungsanlagen sind Anlagen aus Leitungen, insbesondere aus elektrischen Leitungen oder Rohrleitungen, sowie aus den zugehörigen Armaturen, Hausanschlusseinrichtungen, Messeinrichtungen, Steuer-, Regel-, und Sicherheitseinrichtungen, Netzgeräten, Verteilern und Dämmstoffen für die

Leitungen. Zu den Leitungen gehören deren Befestigungen und Beschichtungen. Lichtwellenleiter-Kabel und elektrische Kabel gelten als elektrische Leitungen.

Abweichungen gemäß Art. 81a (1) Satz 2 BayBO sind möglich, wenn mit einer anderen Lösung in gleichem Maße die allgemeinen Anforderungen des Art. 3 Satz 1 erfüllt werden und in der Technischen Baubestimmung eine Abweichung nicht ausgeschlossen ist.

Die Bestandsleitungen müssen entsprechend der zum Zeitpunkt der Errichtung geltenden technischen Baubestimmungen bzw. der bauordnungsrechtlichen Anforderungen hergestellt sein und bei Mängeln entsprechend der heute geltenden Vorgaben ertüchtigt werden.

5.1.3. LÜFTUNGSANLAGEN

Art. 39 BayBO

(1) Lüftungsanlagen müssen betriebssicher und brandsicher sein; sie dürfen den ordnungsgemäßen Betrieb von Feuerungsanlagen nicht beeinträchtigen.

(2) [1]Lüftungsleitungen sowie deren Bekleidungen und Dämmstoffe müssen aus nichtbrennbaren Baustoffen bestehen; brennbare Baustoffe sind zulässig, wenn ein Beitrag der Lüftungsleitung zur Brandentstehung und Brandweiterleitung nicht zu befürchten ist. [2]Lüftungsleitungen dürfen raumabschließende Bauteile, für die eine Feuerwiderstandsfähigkeit vorgeschrieben ist, nur überbrücken, wenn eine Brandausbreitung ausreichend lang nicht zu befürchten ist oder wenn Vorkehrungen hiergegen getroffen sind.

(3) Lüftungsanlagen sind so herzustellen, dass sie Gerüche und Staub nicht in andere Räume übertragen.

(4) [1]Lüftungsanlagen dürfen nicht in Abgasanlagen eingeführt werden; die gemeinsame Nutzung von Lüftungsleitungen zur Lüftung und zur Ableitung der Abgase von Feuerstätten ist zulässig, wenn keine Bedenken wegen der Betriebssicherheit und des Brandschutzes bestehen. [2]Die Abluft ist ins Freie zu führen. [3]Nicht zur Lüftungsanlage gehörende Einrichtungen sind in Lüftungsleitungen unzulässig.

(5) Die Abs. 2 und 3 gelten nicht

1. innerhalb von Gebäuden der Gebäudeklassen 1 und 2,

2. innerhalb von Wohnungen,

3. innerhalb derselben Nutzungseinheit mit insgesamt nicht mehr als 400 m² in nicht mehr als zwei Geschossen.

(6) Für raumlufttechnische Anlagen und Warmluftheizungen gelten die Abs. 1 bis 5 entsprechend.

LüAR

Grundsätzlich müssen Lüftungsanlagen entsprechend Art. 39 BayBO betriebssicher und brandsicher sein. Sollte eine Lüftungsanlage installiert werden, gelten die Regeln der Lüftungsanlagenrichtlinie (LüAR).

Die Richtlinie gilt für den Brandschutz von Lüftungsanlagen, an die Anforderungen nach Art. 39 BayBO gestellt werden. Sie gilt nicht für mit Luft arbeitende Transportanlagen (z.B. Späneabsaugung, Rohrpostanlagen).

Lüftungsanlagen im Sinne der Richtlinie sind auch Klimaanlagen, raumlufttechnische Anlagen und Warmluftheizungen. Lüftungsanlagen bestehen aus Lüftungsleitungen und allen zu ihrer Funktion erforderlichen Bauteilen und Einrichtungen.

Lüftungsleitungen bestehen aus allen von Luft durchströmten Bauteilen, wie Lüftungsrohren, -formstücken, -schächten und -kanälen, Schalldämpfern, Ventilatoren, Luftaufbereitungseinrichtungen, Brandschutzklappen und anderen Absperrvorrichtungen gegen die Übertragung von Feuer und Rauch und Absperrvorrichtungen gegen Rauchübertragung (Rauchschutzklappen) sowie aus ihren Verbindungen, Befestigungen, Dämmschichten, brandschutztechnischen Ummantelungen, Dampfsperren, Folien, Beschichtungen und Bekleidungen.

Abweichungen gemäß den allgemeinen Bestimmungen nach Art. 81a (1) Satz 2 BayBO sind möglich, wenn mit einer anderen Lösung in gleichem Maße die allgemeinen Anforderungen des Art. 3 Satz 1 erfüllt werden und in der Technischen Baubestimmung eine Abweichung nicht ausgeschlossen ist.

Die Bestandsleitungen müssen entsprechend der zum Zeitpunkt der Errichtung geltenden technischen Baubestimmungen bzw. der bauordnungsrechtlichen Anforderungen hergestellt sein und bei Mängeln entsprechend der heute geltenden Vorgaben ertüchtigt werden.

5.1.4. FEUERUNGSANLAGEN, SONSTIGE WÄRMEERZEUGER UND BRENNSTOFFVERSORGUNG

Art 40 BayBO

(1) Feuerstätten und Abgasanlagen (Feuerungsanlagen) müssen betriebssicher und brandsicher sein

Grundsätzlich müssen Feuerstätten im Gebäude betriebssicher und brandsicher gem. FeuV ausgeführt werden. In dem hier betrachteten Bereich ist keine Feuerungsanlage vorhanden. Aufgrund der Nutzungsänderung ergeben sich keine Änderungen an der vorhandenen Feuerungsanalage. Es wird genehmigter Bestand geltend gemacht.

5.1.5. RÄUME ZUR AUFBEWAHRUNG FESTER ABFALLSTOFFE

Räume zur Aufbewahrung fester Abfallstoffe sind im hier betrachteten Bereich nicht vorhanden.

5.1.6. ELEKTRISCHE BETRIEBSRÄUME

In dem hier betrachteten Bereich ist kein elektrischer Betriebsraum vorhanden. Aufgrund der Nutzungsänderung ergeben sich keine Änderungen im Bestand. Es wird genehmigter Bestand geltend gemacht.

5.2 SICHERHEITSTECHNISCHE GEBÄUDEAUSRÜSTUNG

5.2.1. BLITZSCHUTZANLAGEN

Aufgrund der Nutzungsänderung ergeben sich keine Änderungen bezüglich einer Blitzschutzanlage. Es wird genehmigter Bestand für das Gebäude geltend gemacht.

5.2.2. RAUCHWARNMELDER

Art. 46 BayBO

(4) [1]In Wohnungen müssen Schlafräume, Kinderzimmer sowie Flure, die zu Aufenthaltsräumen führen, jeweils mindestens einen Rauchwarnmelder haben. [2]Die Rauchwarnmelder müssen so eingebaut oder angebracht und betrieben werden, dass Brandrauch frühzeitig erkannt und gemeldet wird. [3]Die Eigentümer vorhandener Wohnungen sind verpflichtet, jede Wohnung bis zum 31. Dezember 2017 entsprechend auszustatten. [4]Die Sicherstellung

der Betriebsbereitschaft obliegt den unmittelbaren Besitzern, es sei denn, der Eigentümer übernimmt diese Verpflichtung selbst.

Im betrachteten Gebäude sind keine Wohnungen geplant. Rauchwarnmelder sind bauordnungsrechtlich nicht erforderlich.

5.2.3. RETTUNGSWEGKENNZEICHNUNG

Im hier betrachteten Bereich werden bauordnungsrechtlichen keine Anforderungen an die Kennzeichnung von Rettungswegen gestellt. Es wird jedoch darauf hingewiesen, dass sich aus den geltenden Regeln des Arbeitsstättenrechts weitergehende Anforderungen an die Kennzeichnung von Rettungswegen ergeben können. Eine Überprüfung dieser Anforderungen ist nach § 11 BauVorlV nicht Bestandteil des bauordnungsrechtlichen Brandschutznachweises.

5.2.4. SICHERHEITSBELEUCHTUNG

Eine Sicherheitsbeleuchtung ist für den hier betrachteten Bereich bauordnungsrechtlich nicht erforderlich. Da es sich um eine Arbeitsstätte handelt, wird jedoch darauf hingewiesen, dass sich aus dem geltenden Arbeitsstättenrecht weitergehende Anforderungen ergeben können. Eine Überprüfung und Definition dieser Anforderungen ist nicht Teil des bauordnungsrechtlichen Brandschutznachweises.

5.2.5. BRANDMELDE- UND ALARMIERUNGSANLAGEN

Eine Brandmeldeanlage für die beiden Büroeinheiten ist bauordnungsrechtlich nicht erforderlich.

5.2.6. FEUERLÖSCHEINRICHTUNGEN UND -ANLAGEN

Für die beiden Büroeinheiten sind bauordnungsrechtlich keine Feuerlöscher vorzuhalten.

Da es sich um eine Arbeitsstätte handelt, wird darauf hingewiesen, dass sich aus dem geltenden Arbeitsstättenrecht weitergehende Anforderungen an die Ausstattung mit Feuerlöschern ergeben können. Eine Überprüfung und Definition dieser Anforderungen ist nicht Bestandteil des Brandschutznachweises nach § 11 BauVorlV.

5.2.7. SICHERHEITSSTROMVERSORGUNG

Eine Sicherheitsstromversorgung ist für den hier betrachteten Bereich nicht erforderlich.

5.2.8. FESTSTELLANLAGEN

Selbstschließende Türen mit Anforderungen an den Brandschutz, die aus betrieblichen Gründen offengehalten werden, müssen mit Feststellanlagen versehen werden, die bei Raucheinwirkung ein selbsttätiges Schließen bewirken.

5.2.9. PRÜFUNG SICHERHEITSTECHNISCHER EINRICHTUNGEN

§ 1 SPrüfV – Anwendungsbereich

(1) [1]Diese Verordnung gilt für die Prüfung sicherheitstechnischer Anlagen und Einrichtungen in Sonderbauten (Art. 2 Abs. 4 BayBO) und in Mittel- und Großgaragen (§ 1 Abs. 7 Satz 1 Nrn. 2 und 3 GaStellV), …

Für Sonderbauten sowie Mittel- und Großgaragen ist die Verordnung über die Prüfungen von Sicherheitstechnischen Anlagen und Einrichtungen anzuwenden (§ 1 SPrüfV).

Bauaufsichtlich geforderte sicherheitstechnische Anlagen und Einrichtungen, oder solche Anlagen, an die bauaufsichtliche Anforderungen hinsichtlich des Brandschutzes gestellt werden, sind durch Prüfsachverständige für sicherheitstechnische Anlagen und Einrichtungen für die Prüfung solcher Anlagen auf ihre Wirksamkeit und Betriebssicherheit zu prüfen und zu bescheinigen.

Solche Einrichtungen und Anlagen sind im hier betrachteten Bereich nicht vorhanden.

Des Weiteren sind *sonstige sicherheitstechnisch wichtige Anlagen*, an die bauordnungsrechtliche Anforderungen gestellt werden, insbesondere

- Feuerschutzabschlüsse*
- transportable Feuerlöscher*
- Brandschutzklappen in Lüftungsanlagen*
- automatische Schiebetüren in Rettungswegen*
- Türen mit elektrischen Verriegelungen in Rettungswegen*
- Schutzvorhänge*
- Blitzschutzanlagen*
- trockene Steigleitungen*

zu prüfen.

Die Prüfung mit (*) gekennzeichneten Anlagen kann auch von Sachkundigen nach §2 (3) SPrüfV durchgeführt werden. Die wiederkehrende Prüfung der mit (#) gekennzeichneten Anlagen kann ebenfalls von Sachkundigen nach §2 (3) SPrüfV durchgeführt werden.

Fristen:

- vor der ersten Inbetriebnahme der baulichen Anlage
- unverzüglich nach einer wesentlichen Änderung der baulichen oder der sicherheitstechnischen Anlage/Einrichtung
- wiederkehrend innerhalb einer Frist von drei Jahren (das gilt nicht für die sonstigen sicherheitstechnischen Anlagen)
- je nach Art der sonstigen sicherheitstechnisch wichtigen Anlagen zeitlich unterschiedlich wiederkehrende Prüfung

6 ORGANISATORISCHER BRANDSCHUTZ

Im hier betrachteten Bereich bestehen aus bauordnungsrechtlicher Sicht keine zusätzlichen Anforderungen an den organisatorischen Brandschutz.

Da es sich um eine Arbeitsstätte handelt, wird jedoch darauf hingewiesen, dass sich aus dem geltenden Arbeitsstättenrecht weitergehende Anforderungen ergeben können. Eine Überprüfung und Definition dieser Anforderungen ist nicht Bestandteil des bauordnungsrechtlichen Brandschutznachweises nach § 11 BauVorlV.

Brandlasten

Rettungswege im Gebäude sind generell zu jeder Zeit frei und sicher begehbar zu halten. Einschränkungen hinsichtlich der Brandlasten bestehen nur im notwendigen Treppenraum. Dieser ist zu jederzeit brandlastfrei zu halten.

B ABWEICHUNGSANTRAG

7 GENEHMIGUNGSPFLICHTIGE ABWEICHUNGEN

nach Art. 63 Abs. 1 BayBO

Hinweis

Abweichungen sind **vom Bauherrn zu beantragen** und gelten nur dann als bewilligt, wenn sie im **Genehmigungsbescheid** zum Bauvorhaben **ausdrücklich zugelassen** werden.

Hiermit werden durch den Bauherrn folgende Abweichungen beantragt.

7.1 ABWEICHUNG VON KAPITEL 4.3.5 - NOTWENDIGE TREPPENRÄUME

Bauordnungsrechtliche Anforderung

Art. 33 BayBO

(1) [1]Jede notwendige Treppe muss zur Sicherung der Rettungswege aus den Geschossen ins Freie in einem eigenen, durchgehenden Treppenraum liegen (notwendiger Treppenraum). [2]Notwendige Treppenräume müssen so angeordnet und ausgebildet sein, dass die Nutzung der notwendigen Treppen im Brandfall ausreichend lang möglich ist. [3]Notwendige Treppen sind ohne eigenen Treppenraum zulässig

1. in Gebäuden der Gebäudeklassen 1 und 2,

2. für die Verbindung von höchstens zwei Geschossen innerhalb derselben Nutzungseinheit von insgesamt nicht mehr als 200 m2, wenn in jedem Geschoss ein anderer Rettungsweg erreicht werden kann,

3. als Außentreppe, wenn ihre Nutzung ausreichend sicher ist und im Brandfall nicht gefährdet werden kann.

Ausführung/Abweichung

Die notwendige Treppe im hier betrachteten Bereich „Büro 1" soll ohne eigenen notwendigen Treppenraum errichtet werden. Die hier betrachtete offene Treppe erstreckt sich über zwei Geschosse mit einer Brutto-Grundfläche von ca. 120 m². Für den fehlenden weiteren Rettungsweg aus dem hier betrachteten Kellergeschossbereich gem. Art. 33 (1) Nr. 2 BayBO wird eine Abweichung beantragt.

Begründung/Kompensation

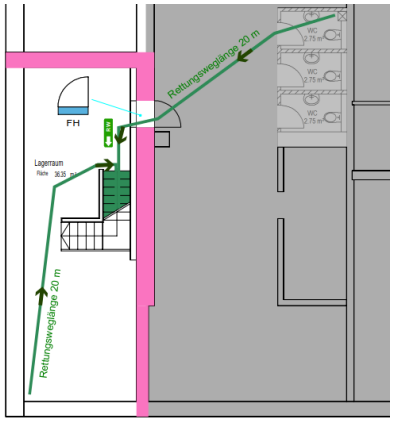

Aus brandschutztechnischer Sicht kann die Abweichung akzeptiert werden, da es sich bei den hier betrachteten Räumen im Kellergeschoss (Lagerraum und WC) um keine Aufenthaltsräume handelt und auch keine Aufenthaltsräume zulässig sind.

GUTACHTERL. ZUSAMMENFASSUNG / ABSCHLIEßENDE STELLUNGNAHME

Für das hier betrachtete Bauvorhaben hat das Unterzeichnerbüro vorstehend einen brandschutztechnischen Nachweis zur Vorlage im Baugenehmigungsverfahren aufgestellt. Beurteilungsgrundlage war dabei im Wesentlichen die **Bayerische Bauordnung (BayBO).** Im Zuge des Brandschutznachweises wurde lediglich die Konformität mit dem öffentlichen Baurecht geprüft. Auf die Hinweispflicht des Architekten bzw. zuständigen Fachplaners bei Abweichungen von anerkannten Regeln der Technik gegenüber dem Bauherrn wird hingewiesen.

Zusammenfassend kann festgestellt werden, dass gegen die Baumaßnahme sowie die Nutzung und insbesondere auch gegen die Genehmigung der beantragten Abweichungen dann

keine brandschutztechnischen Bedenken

bestehen, wenn jede der im Brandschutznachweis genannten Sicherheitsvorkehrungen und Schutzmaßnahmen in vollem Umfang umgesetzt wird.

Im Übrigen gelten die vorangegangenen Betrachtungen ausschließlich für das konkret bewertete Objekt sowie den genannten Planstand, d.h. eine Übertragung auf andere Objekte oder Planstände ist ohne vorherige Prüfung des Unterzeichners nicht möglich.

Für die Umsetzung des Brandschutzkonzeptes ist der Bauherr, in Verbindung mit seinem Beauftragten (Planer, Fachplaner, Bauleiter, usw.) verantwortlich.

Ausgestellt:

Sulzberg, den 06.02.2019

.....

Lena Buch
(B.Eng. Bauingenieurwesen)

.....

Elmar König
(Dipl. Ing. (FH), MEng Brandschutz, Nachweisberechtigter für vorbeugenden Brandschutz)

Der Brandschutznachweis setzt nicht automatisch die vollumfängliche Genehmigungsfähigkeit ohne weitere Anforderungen und Auflagen voraus.

Der Brandschutznachweis gemäß Art. 64 Abs. 4 BayBO wurde zur Kenntnis genommen.

Hiermit wird die Genehmigung der beschriebenen Abweichungen beantragt.

Ort: .....

Datum: .....

Unterschrift der **Bauherrschaft**: .....

Ort: .....

Datum: .....

Unterschrift des **Entwurfsverfassers**: .....

Anlagen

- Brandschutzkonzeptplan

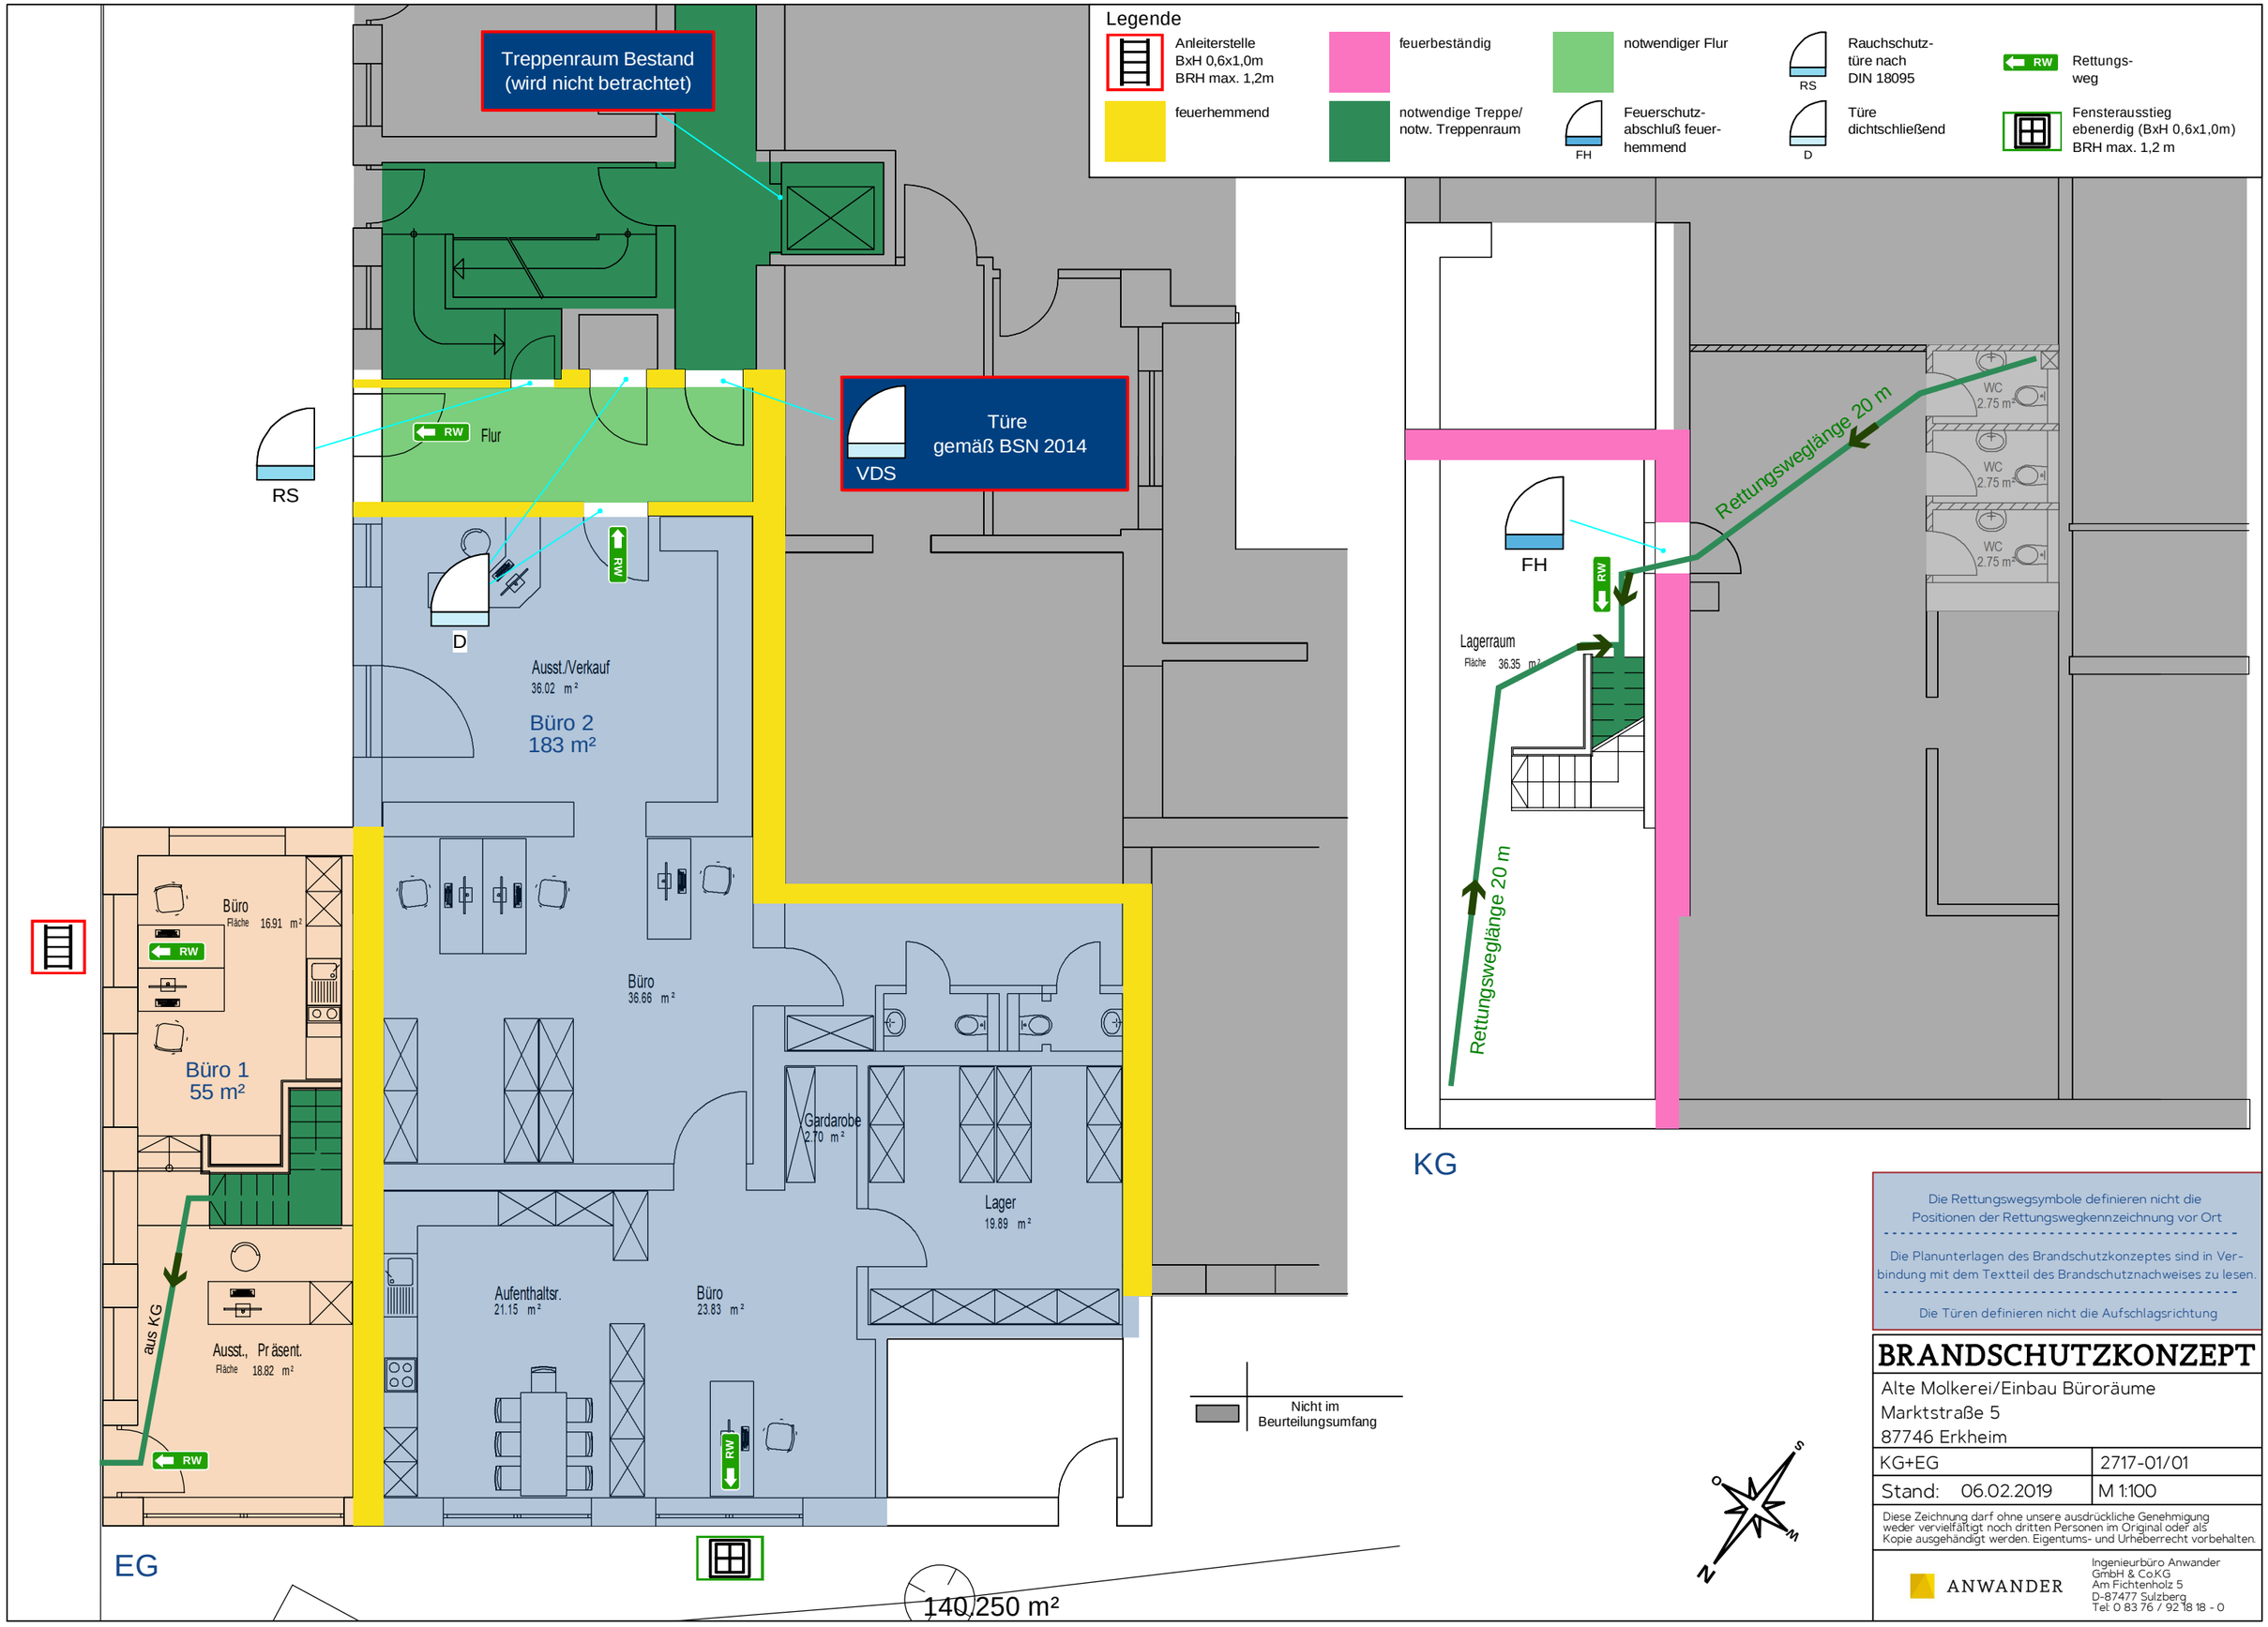
Legende
Anleiterstelle BxH 0,6x1,0m BRH max. 1,2m
feuerhemmend
feuerbeständig
notwendige Treppe/ notw. Treppenraum
notwendiger Flur
Feuerschutz-abschluß feuer-hemmend
FH
Rauchschutz-türe nach DIN 18095
RS
Türe dichtschließend
D
Rettungs-weg
RW
Fensterausstieg ebenerdig (BxH 0,6x1,0m) BRH max. 1,2 m
Treppenraum Bestand (wird nicht betrachtet)
Türe gemäß BSN 2014
VDS
RS
Flur
D
Ausst./Verkauf
36.02 m²
Büro 2
183 m²
Büro
Fläche 16.91 m²
Büro 1
55 m²
Ausst., Präsent.
Fläche 18.82 m²
aus KG
Büro
36.66 m²
Gardarobe
2.70 m²
Lager
19.89 m²
Aufenthaltsr.
21.15 m²
Büro
23.83 m²
Nicht im Beurteilungsumfang
EG
140,250 m²
FH
Lagerraum
Fläche 36.35 m²
Rettungsweglänge 20 m
Rettungsweglänge 20 m
WC 2.75 m²
WC 2.75 m²
WC 2.75 m²
KG
Die Rettungswegsymbole definieren nicht die Positionen der Rettungswegkennzeichnung vor Ort
Die Planunterlagen des Brandschutzkonzeptes sind in Verbindung mit dem Textteil des Brandschutznachweises zu lesen.
Die Türen definieren nicht die Aufschlagsrichtung
BRANDSCHUTZKONZEPT
Alte Molkerei/Einbau Büroräume
Marktstraße 5
87746 Erkheim
KG+EG
2717-01/01
Stand: 06.02.2019
M 1:100
Diese Zeichnung darf ohne unsere ausdrückliche Genehmigung weder vervielfältigt noch dritten Personen im Original oder als Kopie ausgehändigt werden. Eigentums- und Urheberrecht vorbehalten.
ANWANDER
Ingenieurbüro Anwander GmbH & CoKG
Am Fichtenholz 5
D-87477 Sulzberg
Tel: 0 83 76 / 92 18 18 - 0